
ARCHITECTURAL
PORTFOLIO

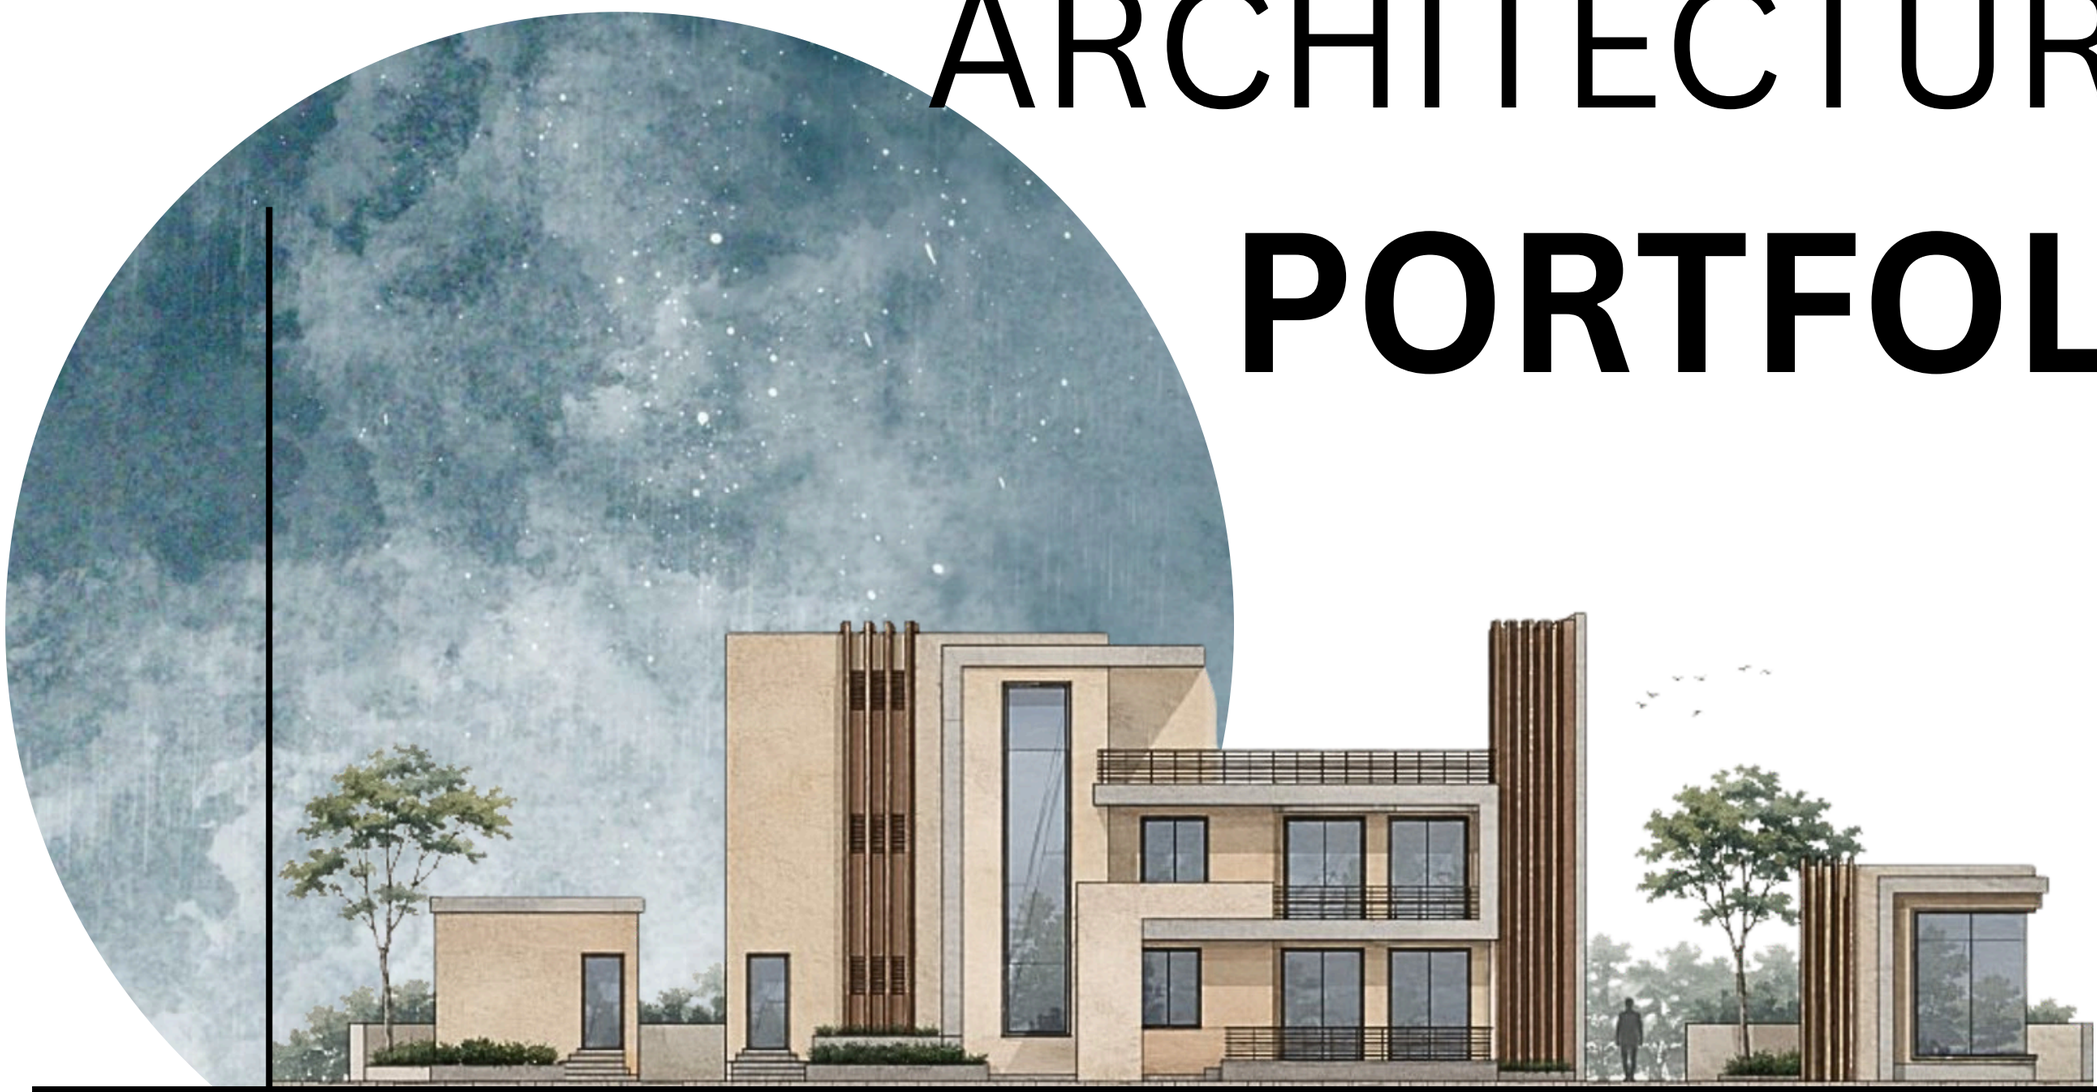

2023 — 2026

Beyond the Conventional

Vishakha Bharti



ABOUT.

HELLO I am Vishakha Bharti a fourth year student doing my Bachelors in architecture at IIT Kharagpur, and I am still learning what it means to truly listen to a space. Architecture, for me, is not simply about building — it is about understanding the quiet negotiations between people and the places they inhabit, between structure and sky, between what a site demands and what a person needs.

I am drawn to the moments where design becomes almost invisible — where a threshold feels natural, where light falls exactly as it should, where a room holds its occupant without announcing itself. I want to understand how those moments are made, and how to make them deliberately.

I sketch because thinking slows down when my hand moves. I observe because every built thing has an argument embedded in it. And I design because I believe that space, at its most honest, can hold the full complexity of a human life.

vishakha8642@gmail.com
vishakha8642@kgpian.iitkgp.ac.in

_vishakha_1_

https://www.linkedin.com/in/vishakha-bharti-54b9b2292/

EDUCATION

2023-Present — **Bachelor of Architecture**
Indian Institute of Technology Kharagpur, Kharagpur, W.B.
CGPA: 8.4

2020-2022 — **Higher Secondary Education**
Sanfort World School, Moradabad, U.P.

2012-2020 — **Secondary Education**
S S Children Academy Girls School, Moradabad, U.P.

EXPERIENCE

Product and Architectural Intern (May'25 - Jul’25)
Veshmn Innovation Private Limited, Guragaon, Haryana
Structured design databases, developed 10+ 3D models and visualizations, and created client-ready presentations to streamline workflows and enhance design communication.

Architectural and Interior Design Intern (May'26 - Aug’26)
SoCH Studio of Creative Heads, Guragaon, Haryana
Prepared CAD drawings, developed interior design concepts and mood boards, created 3D models and visualizations, and participated in client meetings to communicate and refine design requirements.

INTERESTS

Painting
Sketching
Skating
Roller Ball
Badminton

LANGUAGE

- English
- Hindi

SKILLS

Professional
Strong critical thinking and problem-solving abilities, complemented by effective design communication, teamwork, leadership, organization, and presentation skills. Demonstrates a responsible, adaptable, and collaborative approach to projects, with a keen ability to develop and communicate ideas effectively.

Sofware

Drafting
- AutoCAD

BIM
- REVIT

3D Modelling
- SketchUp
- Rhino

Presentation
- Canva
- Microsoft Excel
- Microsoft Word


Visualization
- D5
- ENSCAPE
- V-Ray
- Lumion

Graphics
- Adobe Photoshop
- Canva
- Adobe Illustrator
- Indesign

COMPETITIONS

- Achieved 1nd Place in D24, a 24-hour Design challenge conducted by the Department of Architecture and Regional Planning, IIT Kharagpur
- Awarded 2nd Prize in a Time-Constrained Design Test, jointly conducted by IIT Kharagpur and Jadavpur University
- Awarded 3rd Prize in a Time-Constrained Design Test, jointly conducted by IIT Kharagpur and IIEST Shibpur
- Secured 1st Position in Earthquake-Resistant Architectural and Structural Design conducted by the Department of Architecture and Regional Planning, IIT Kharagpur
- Represented IIT Kharagpur as a ZONASA Delegate in 2024 and 2025 participated in D24, 3D Modelling and various architectural competitions, along with workshops and design-related events.

CONTENT

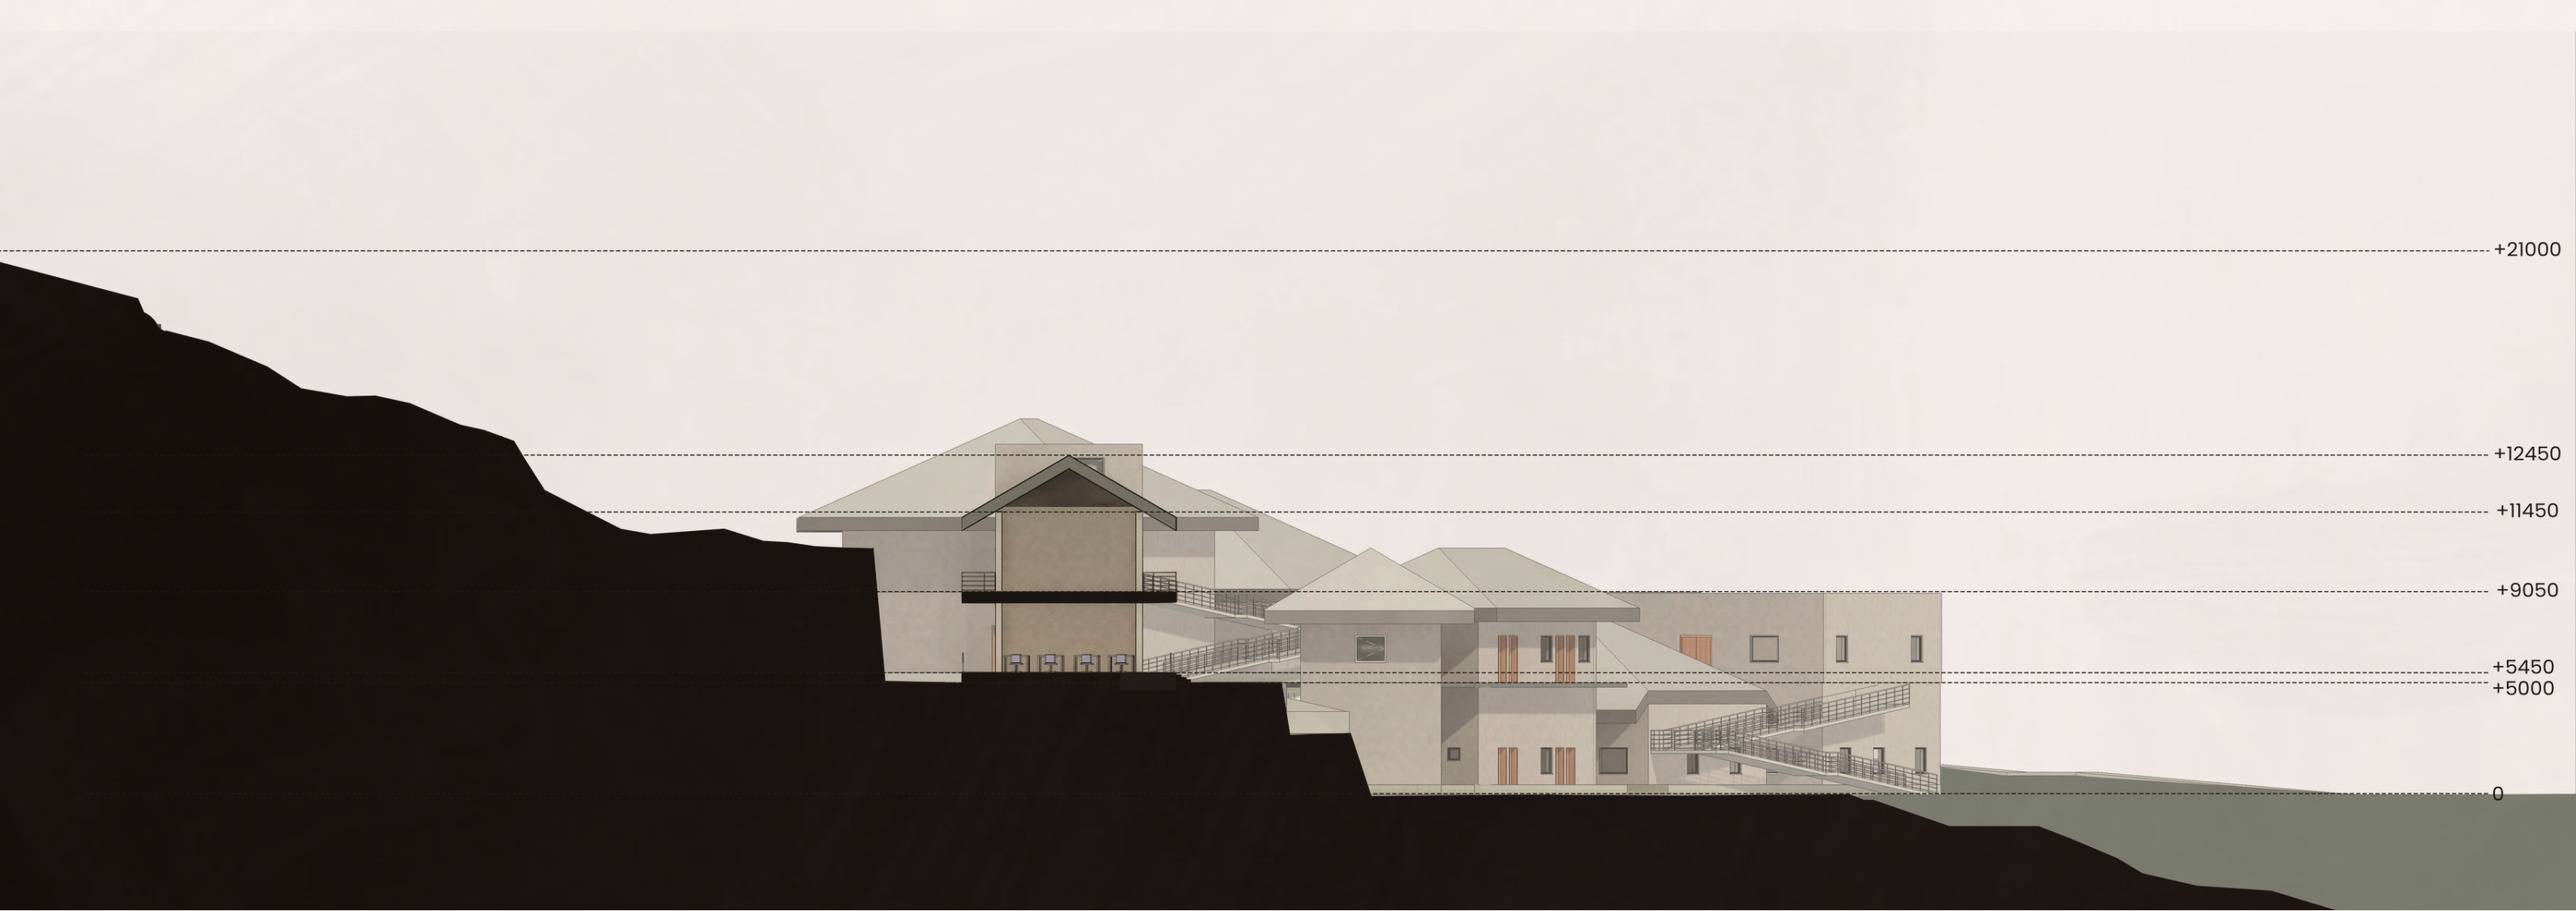


01.




BEACH RESORT
(Academic Work)

02.

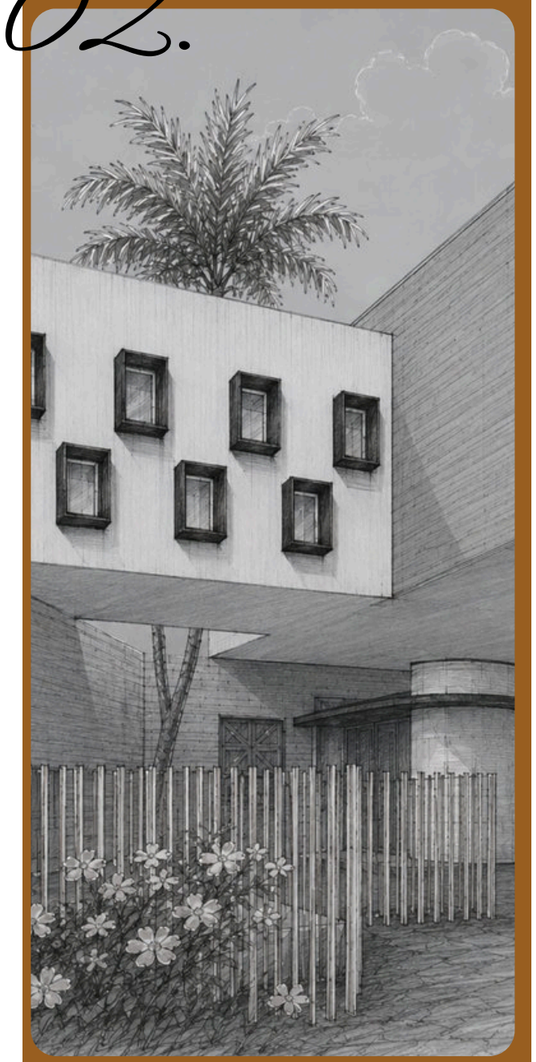


MUSEUM
(Academic Work)

03.

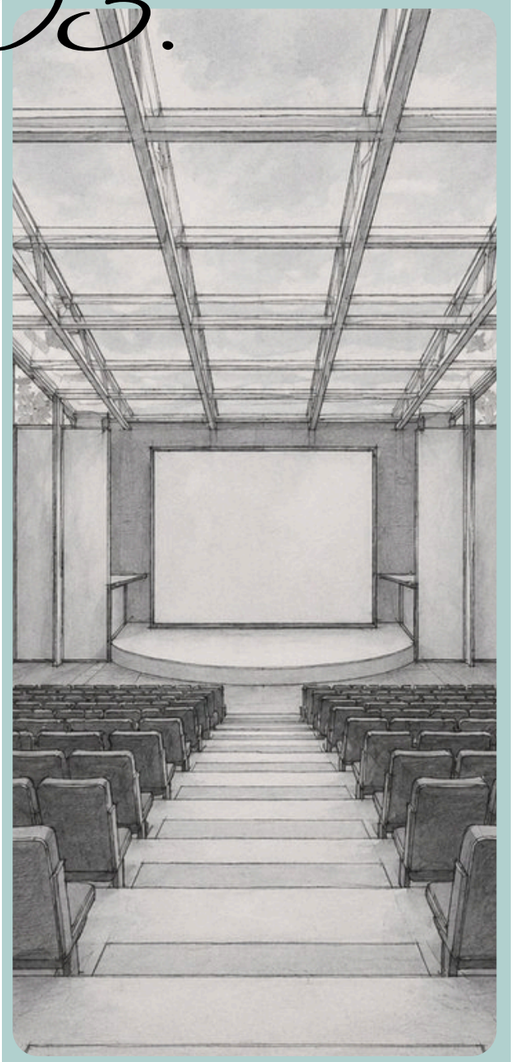


COMMUNITY CENTRE
(Academic Work)

04.

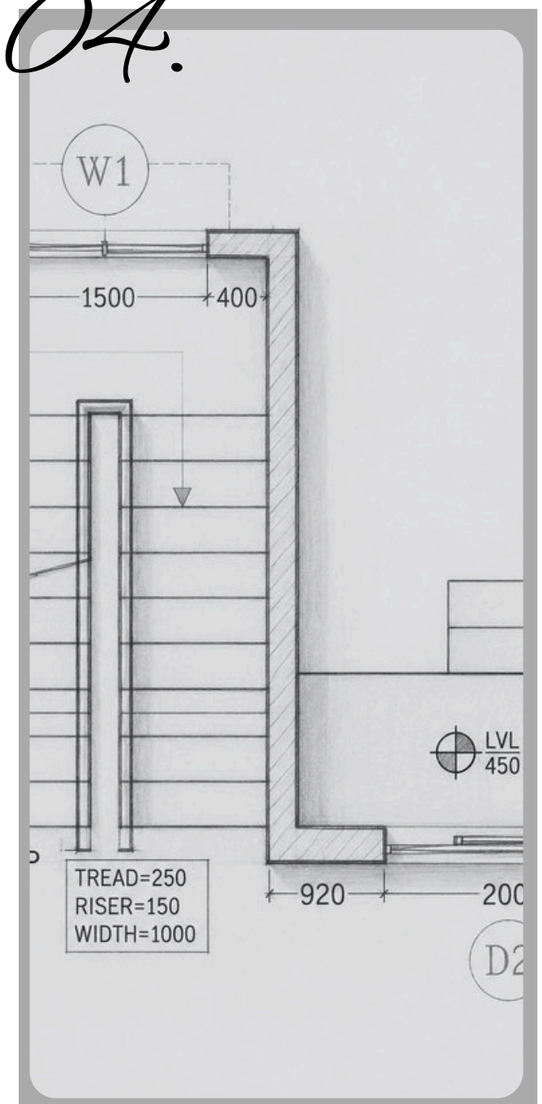

MISCELLANEOUS
(Academic + Intern Work)



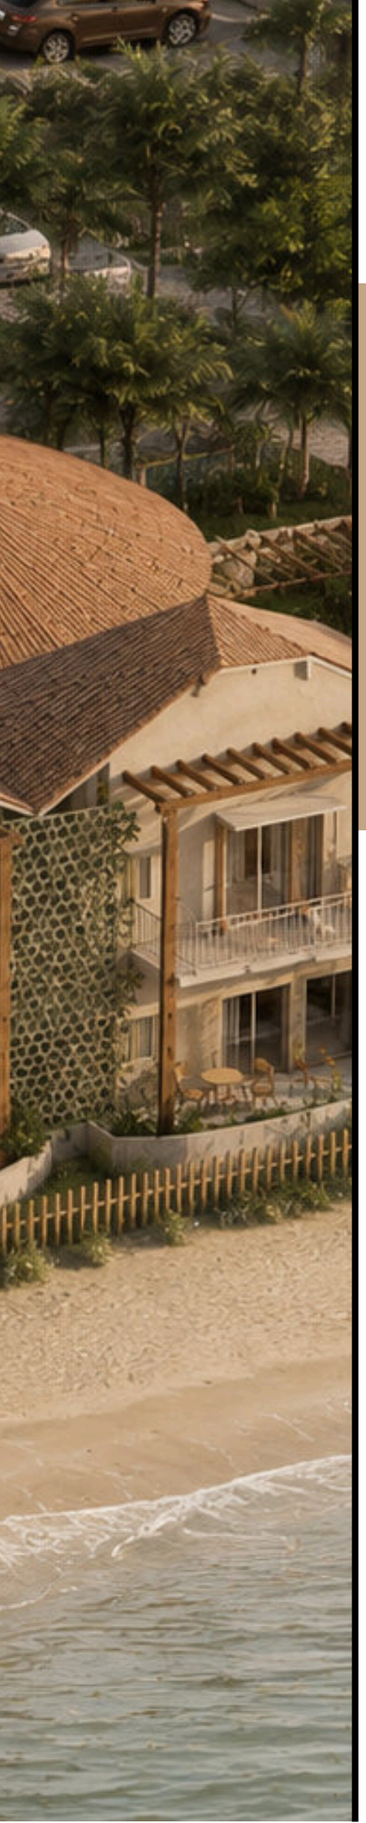

THENDRAL MARABU

Chennai, Tamil Nadu

In a coastal city where the relationship between people and the sea is ancient and unhurried, this resort was designed not as an escape from place but as a deeper entry into it. Chennai's shoreline carries a particular quality of wind the Thendral that moves through coconut groves, fishing villages, and temple courtyards before it reaches the water's edge. This resort was designed to catch that wind deliberately, to let it move through every corridor, every verandah, every shaded outdoor space as though the building had always been a part of the landscape it sits within.

Thendral Marabu is not simply a place to stay. It is an attempt to translate the rhythm of coastal Tamil heritage into built form where materiality, orientation, and spatial sequence together tell the story of a shoreline that has been lived in for centuries. A resort where arriving feels less like checking in and more like coming home to something you did not know you remembered.

CONCEPT

Heritage, Nature, Tranquility


THE COAST




LOCAL HERITAGE




DESIGN INTENT

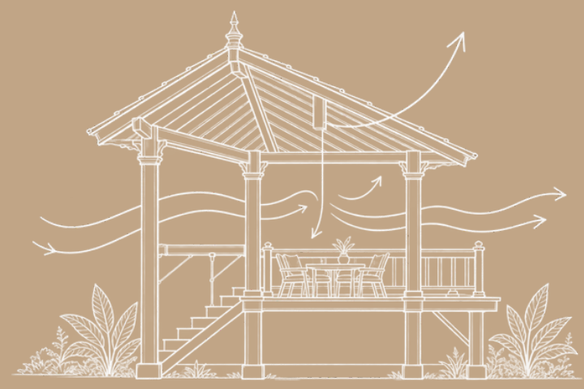

THE EXPERIENCE

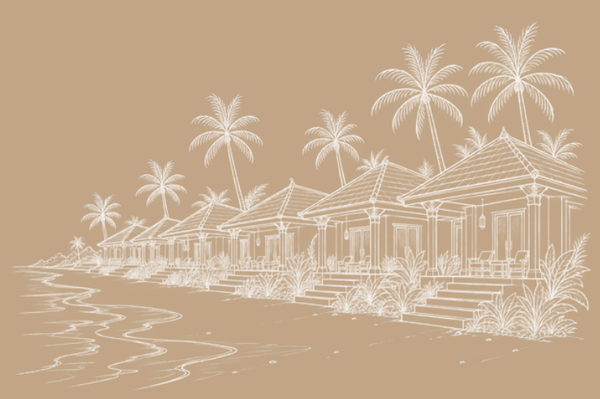

ROOTED IN HERITAGE

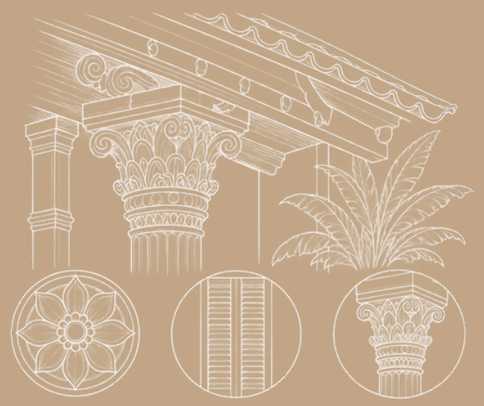

Local Architecture, Materials and Craftsmanship

IN HARMONY WITH NATURE



Lush Landscaping, natural textures and calm spaces

SENSE OF TRANQUILITY




Natural Light, Shadows and Soothing spaces

EXPERIENCE THE COAST




Moments of relaxation and connection

A timeless retreat where heritage meets the sea...

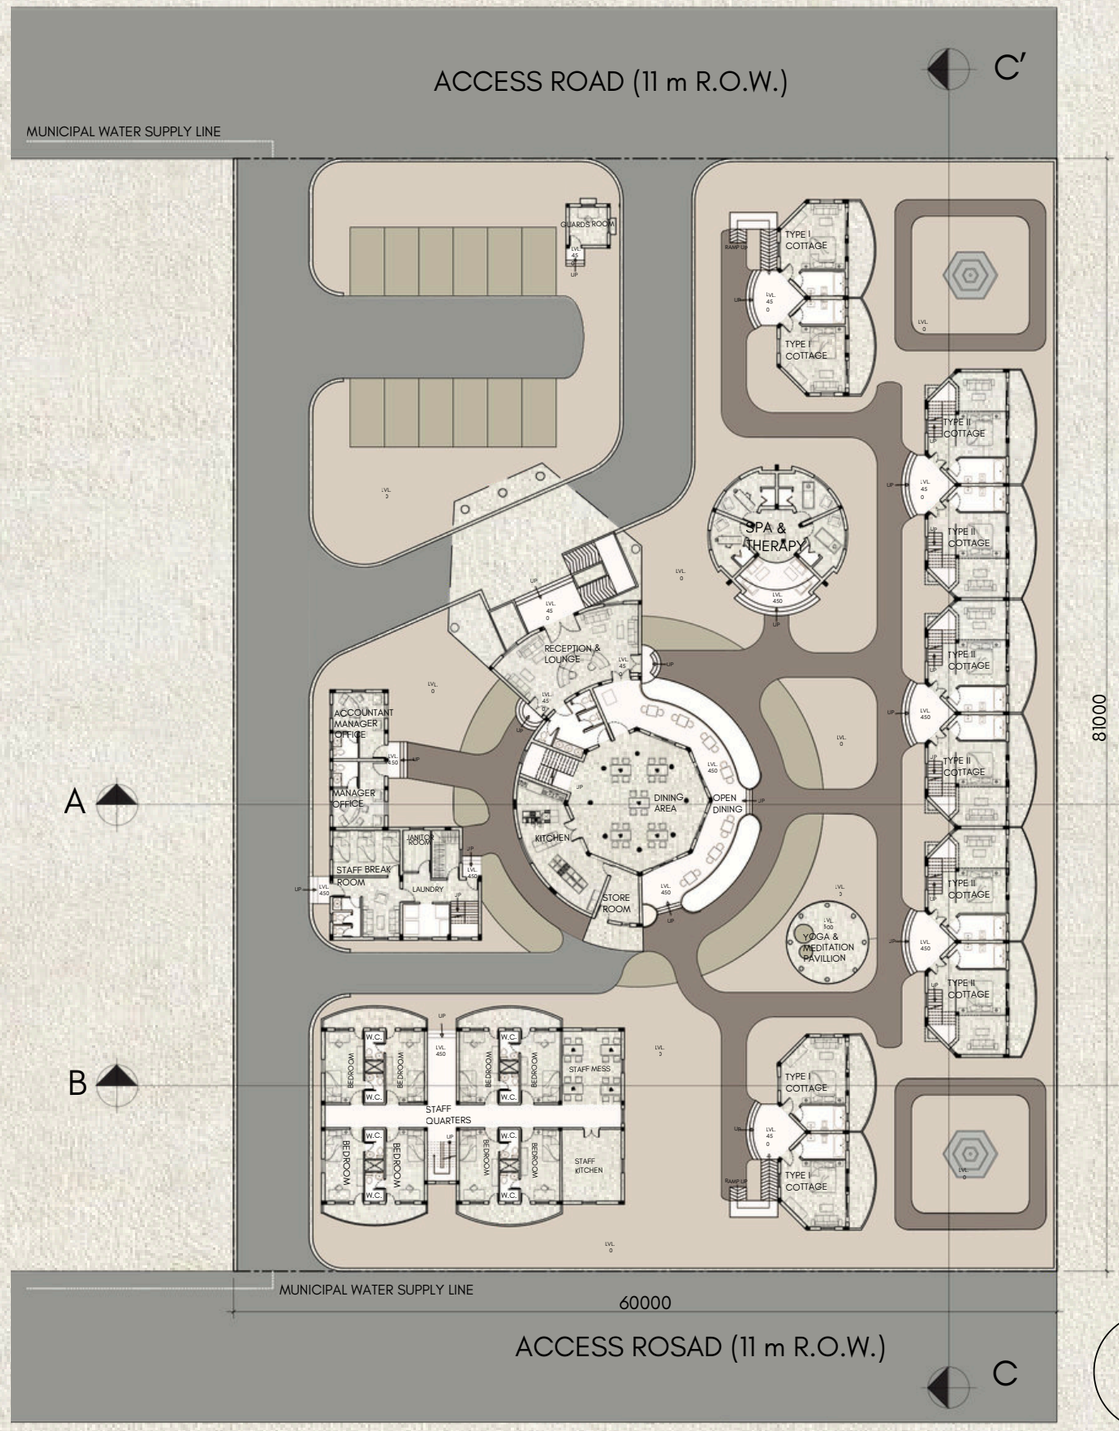
ACCESS ROAD (11 m R.O.W.)
C′
MUNICIPAL WATER SUPPLY LINE
GUARDS ROOM
TYPE I COTTAGE
TYPE I COTTAGE
TYPE II COTTAGE
TYPE II COTTAGE
TYPE II COTTAGE
TYPE II COTTAGE
TYPE II COTTAGE
SPA & THERAPY
RECEPTION & LOUNGE
ACCOUNTANT MANAGER OFFICE
MANAGER OFFICE
JANITOR ROOM
STAFF BREAK ROOM
LAUNDRY
KITCHEN
DINING AREA
OPEN DINING
STORE ROOM
YOGA & MEDITATION PAVILLION
STAFF QUARTERS
BEDROOM
W.C.
STAFF MESS
STAFF KITCHEN
TYPE I COTTAGE
TYPE I COTTAGE
A
A′
B
B′
81000
MUNICIPAL WATER SUPPLY LINE
60000
ACCESS ROSAD (11 m R.O.W.)
C
N


ACCESS ROAD (11 m R.O.W.)
C′
MUNICIPAL WATER SUPPLY LINE
TYPE II COTTAGE
RECEPTION & LOUNGE
W.C.
CAFE & BAR
KITCHEN
STORE ROOM
STAFF QUARTERS
BEDROOM
W.C.
A
A′
B
B′
81000
MUNICIPAL WATER SUPPLY LINE
60000
ACCESS ROADS (11 m R.O.W.)
C

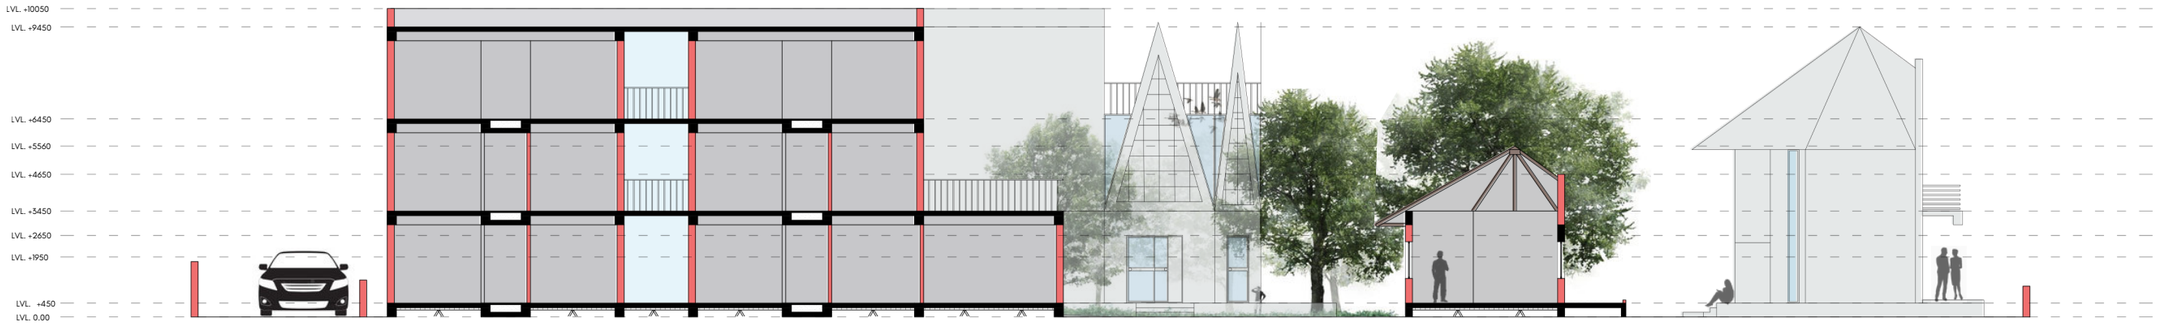

SECTION AA'



SECTION BB'



SECTION CC'














BANGLAR SHILPO GHAR

Kolkata, West Bengal

In a country where folk art does not hang in galleries but lives in the hands of the people who make it, this museum was designed to close that distance. Banglar Shilpo Ghar, the House of Bengal's Craft is rooted in the visual language of the land it celebrates: terracotta patterns borrowed from temple facades, bamboo screens that filter light the way a Kantha stitch filters colour, open courtyards that echo the rhythm of a village maidan.

The building is organised around three galleries Folk Art, Folk Music, and Folk Handcraft each unfolding as a sensory journey rather than a simple display. Light, texture, sound, and material work together to create an experience that does not just show Bengali heritage but lets visitors feel its weight and warmth. This is a building that does not merely house culture it participates in it, quietly and with conviction.

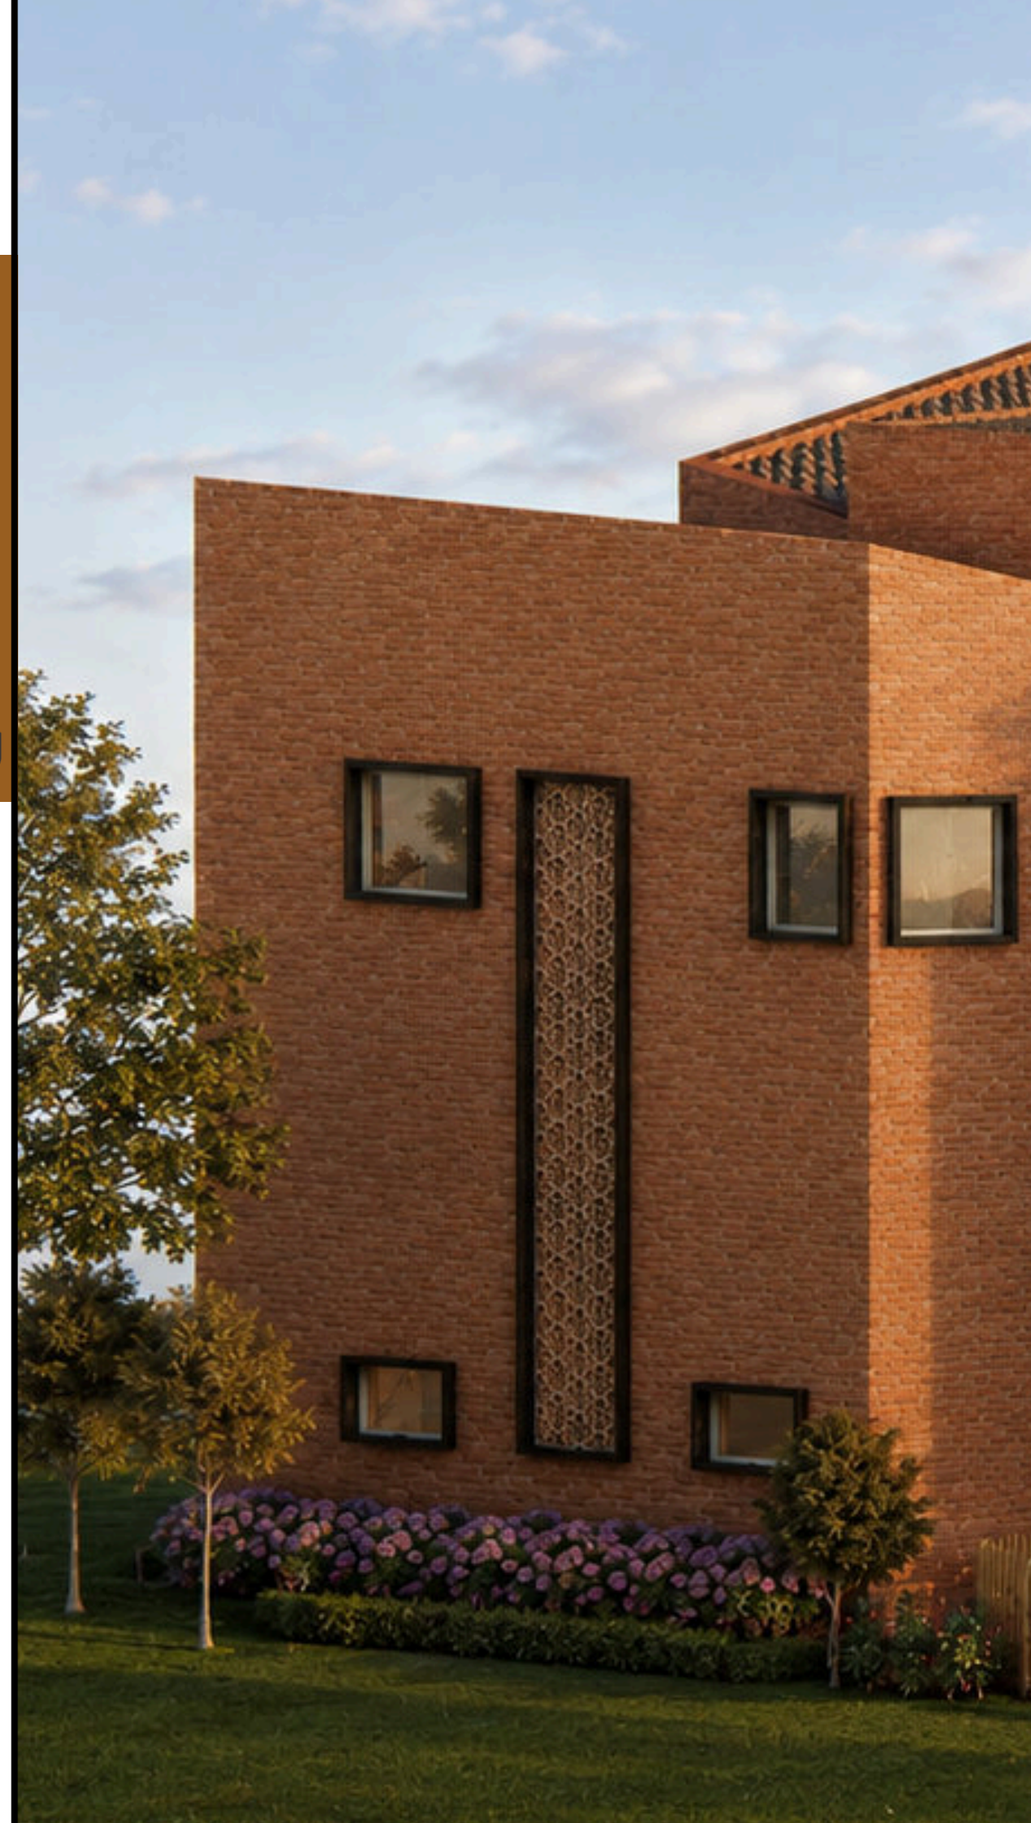


FLOOR PLANS



GROUND FLOOR PLAN



FIRST

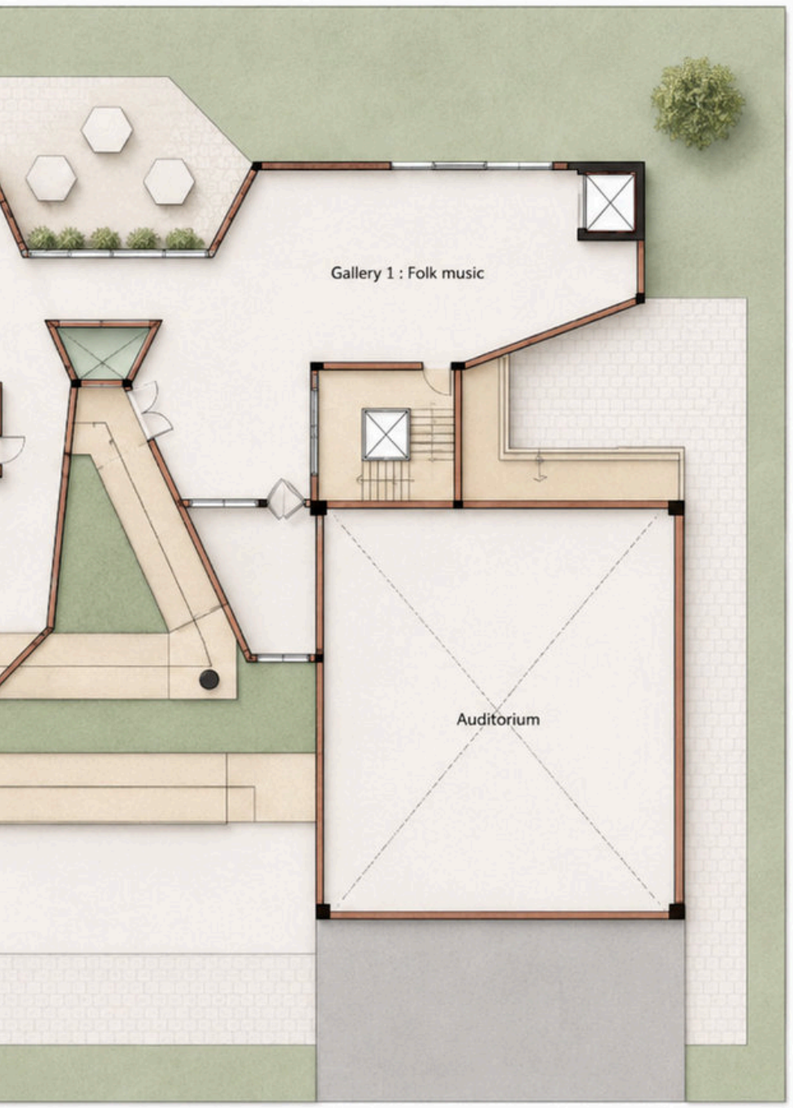




FLOOR PLAN


SECOND FLOOR PLAN


N




Banglar Shilpo Ghar is conceived as a journey through Bengal's cultural identity, beginning with its folk traditions and evolving into spaces dedicated to art, music and craft. The design translates these cultural influences into a contemporary architectural experience, where movement through the galleries, auditorium, workshop and café allows visitors to gradually discover and engage with Bengal's artistic heritage.

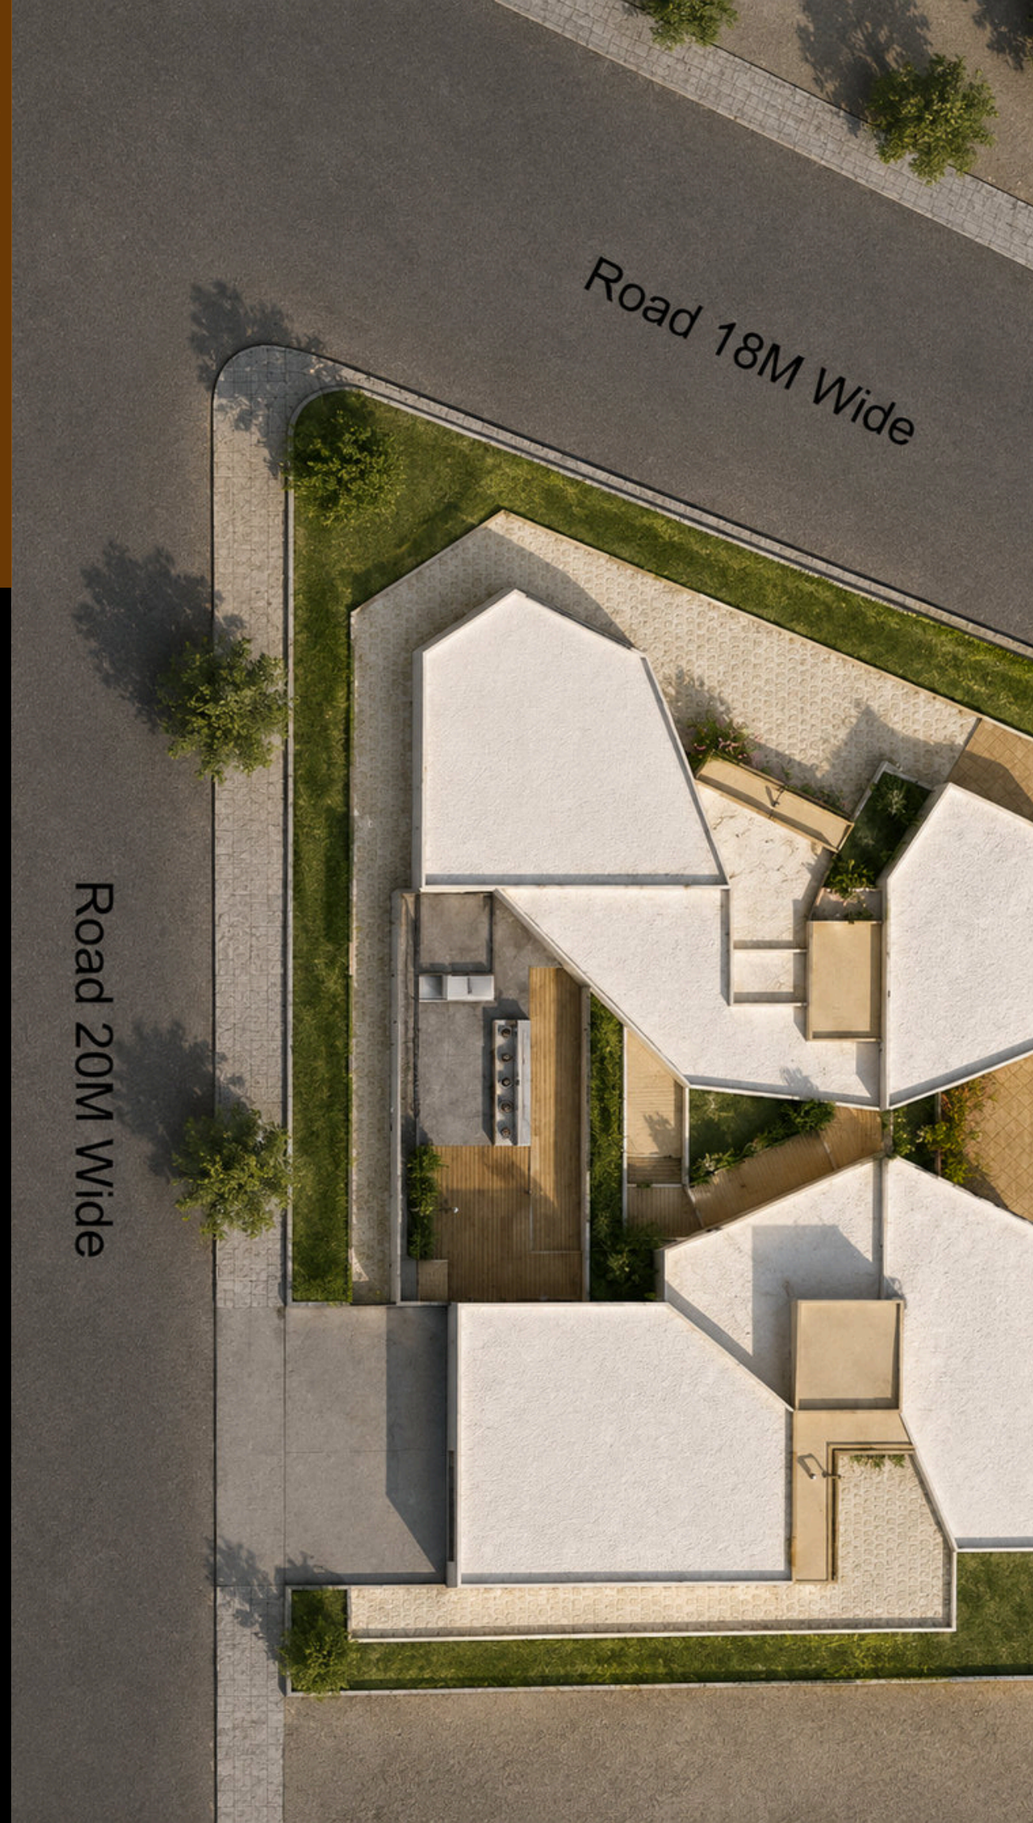

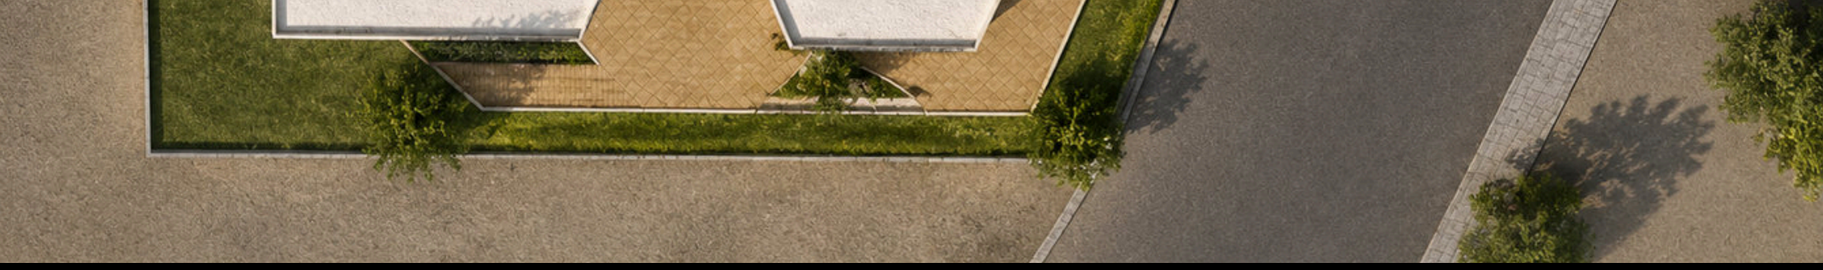


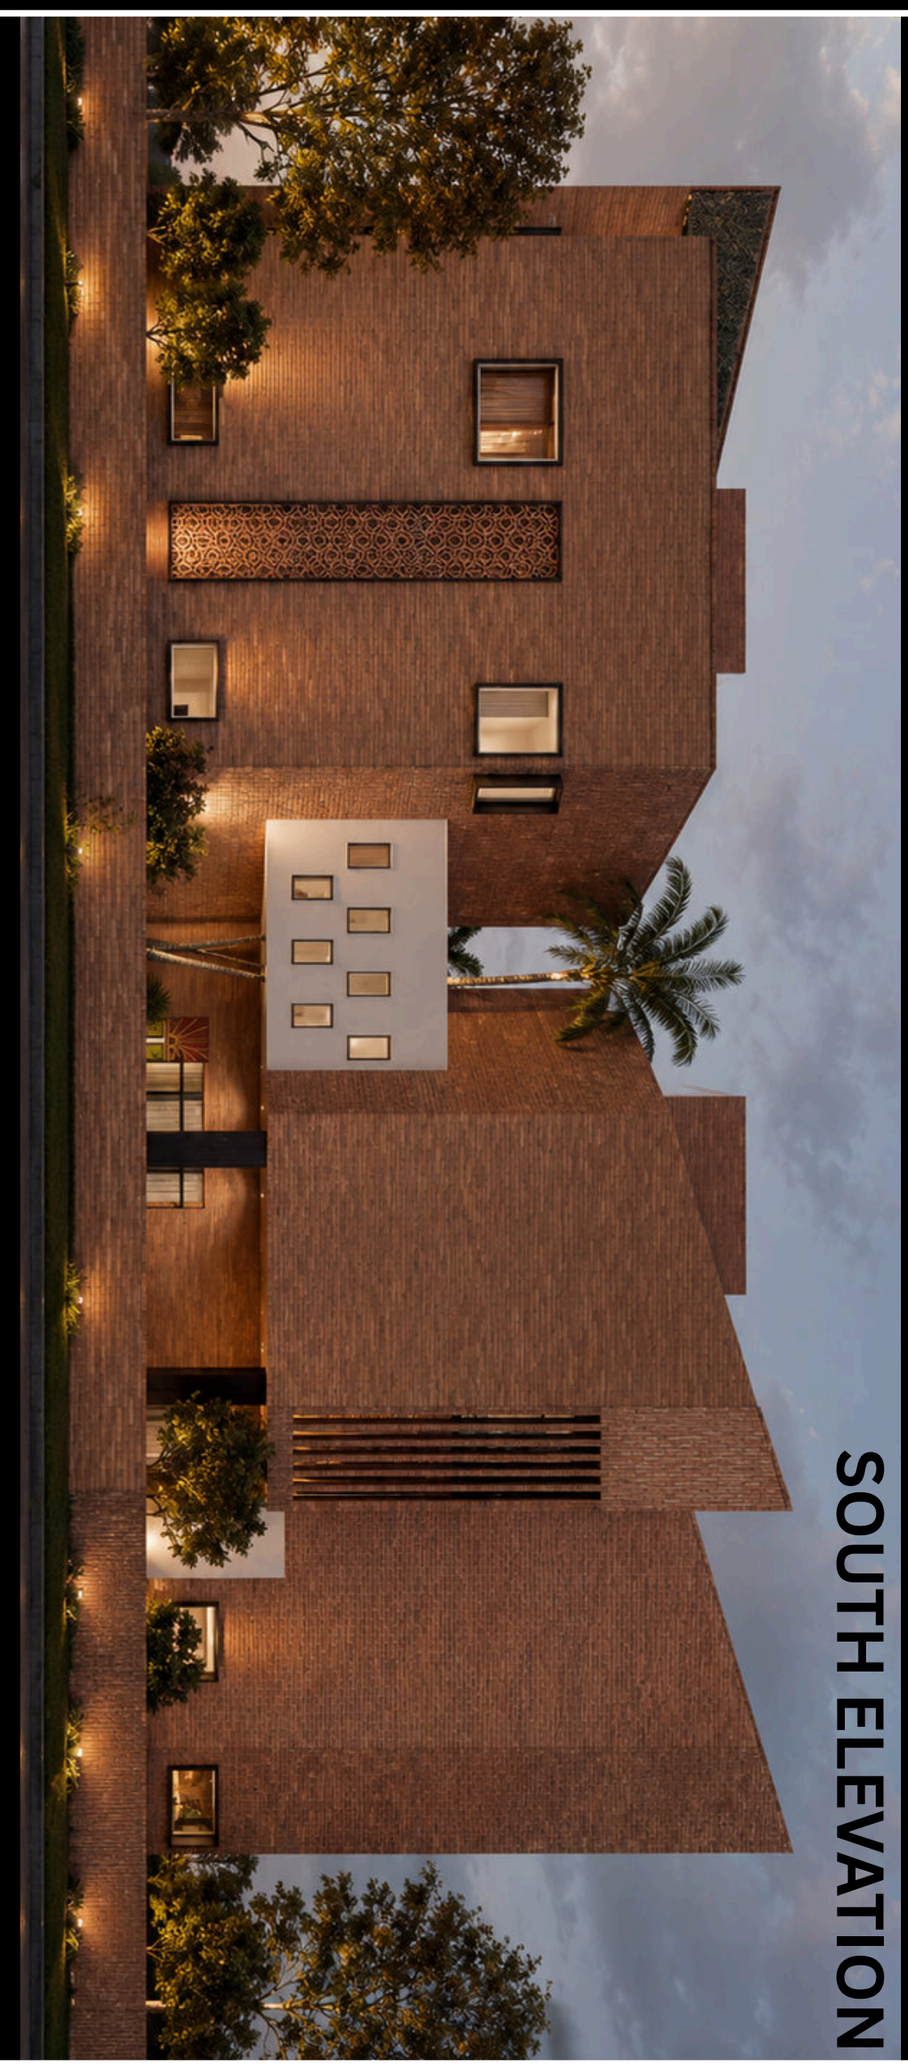

SOUTH ELEVATION

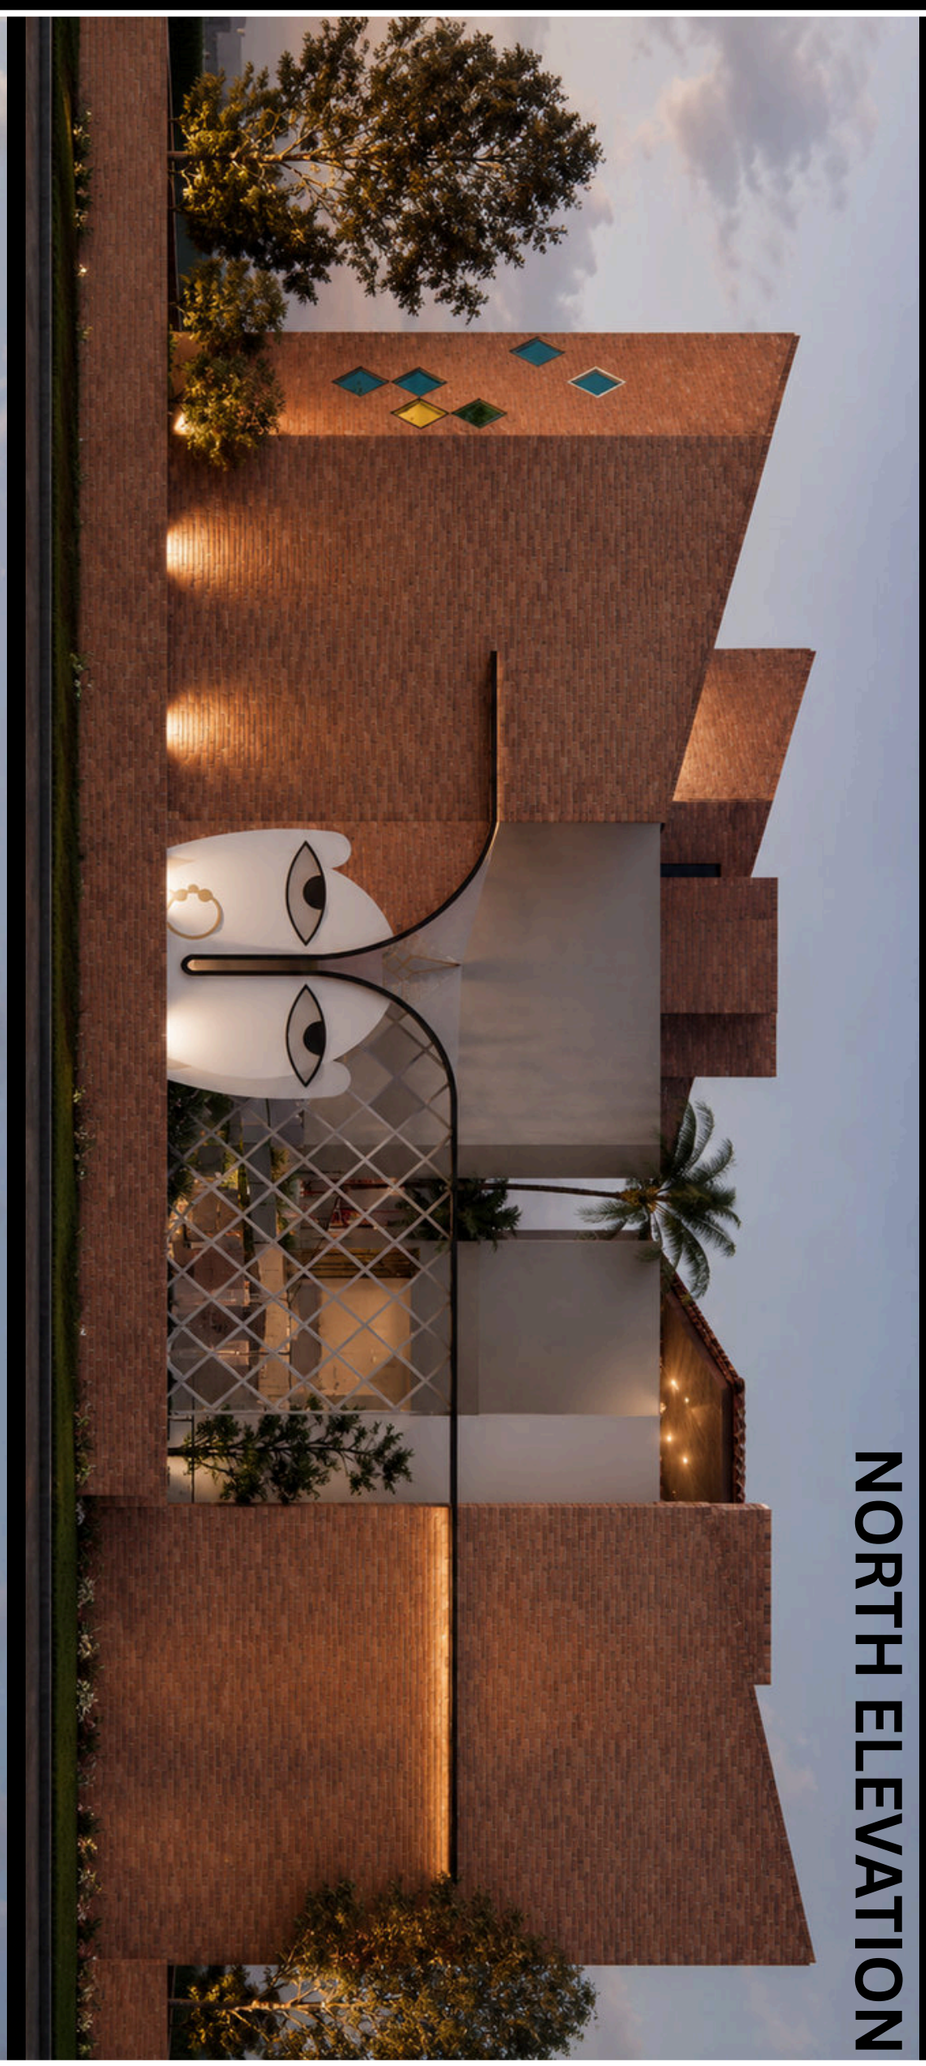


NORTH ELEVATION

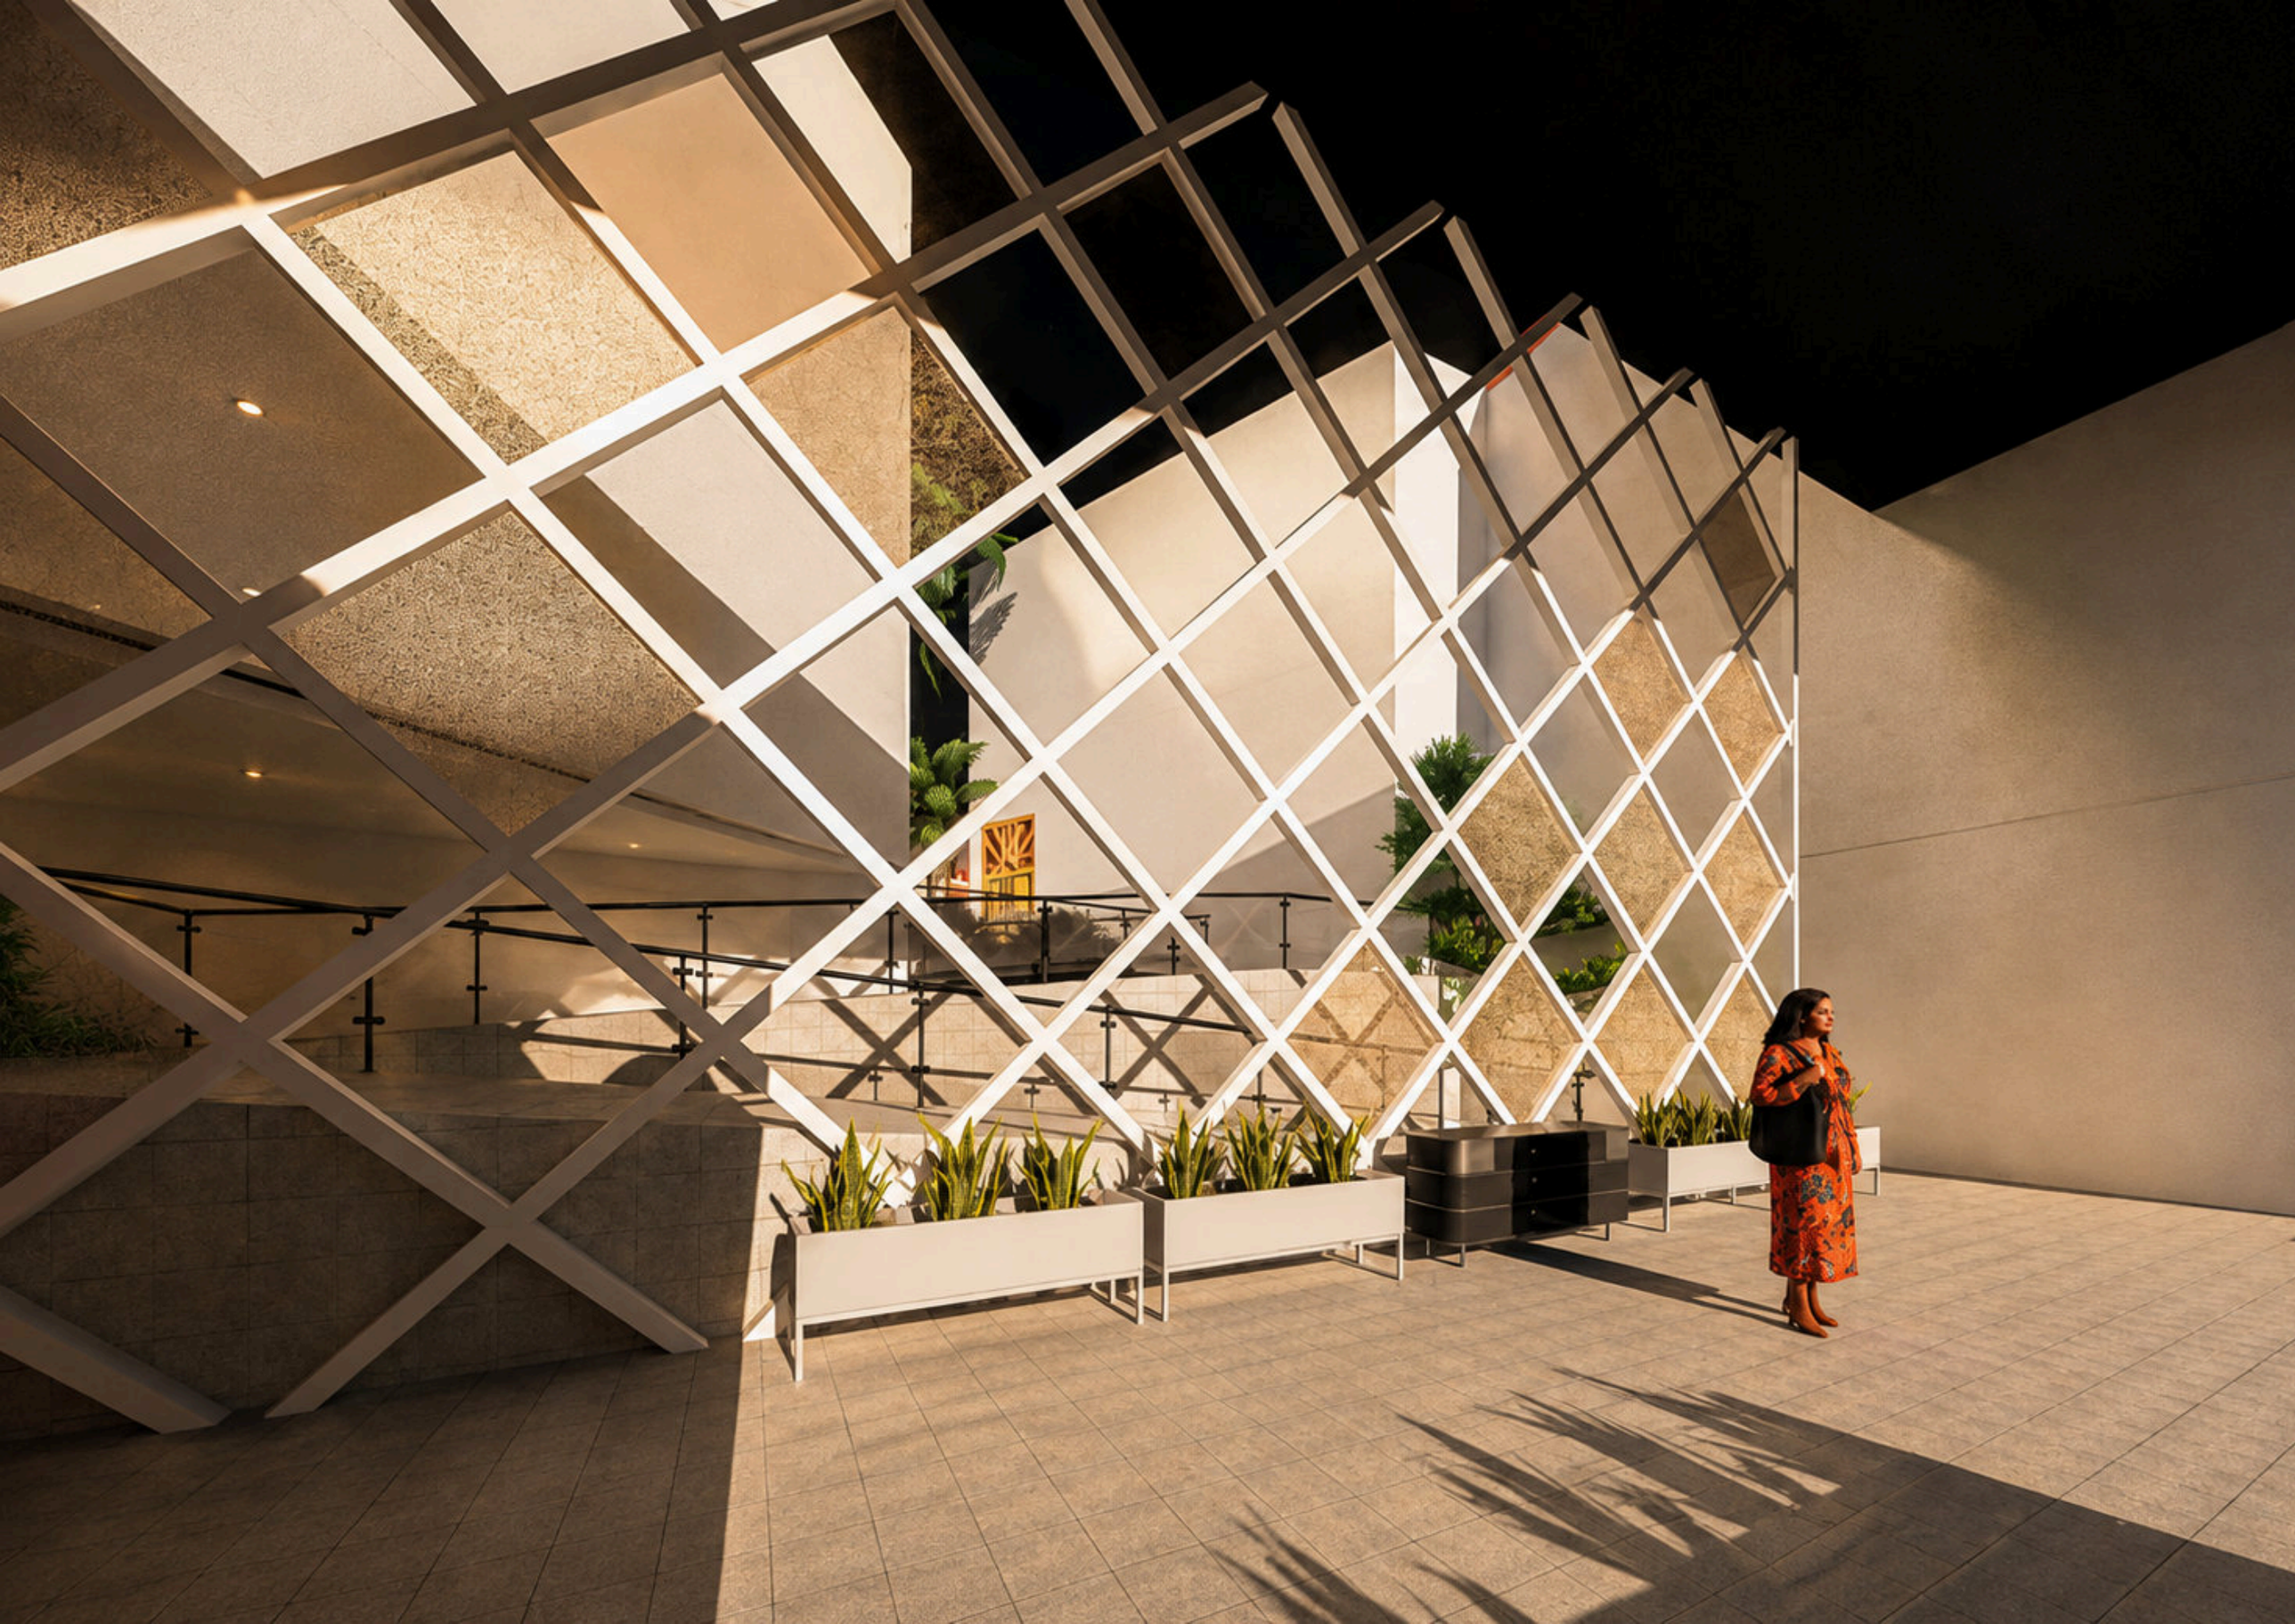





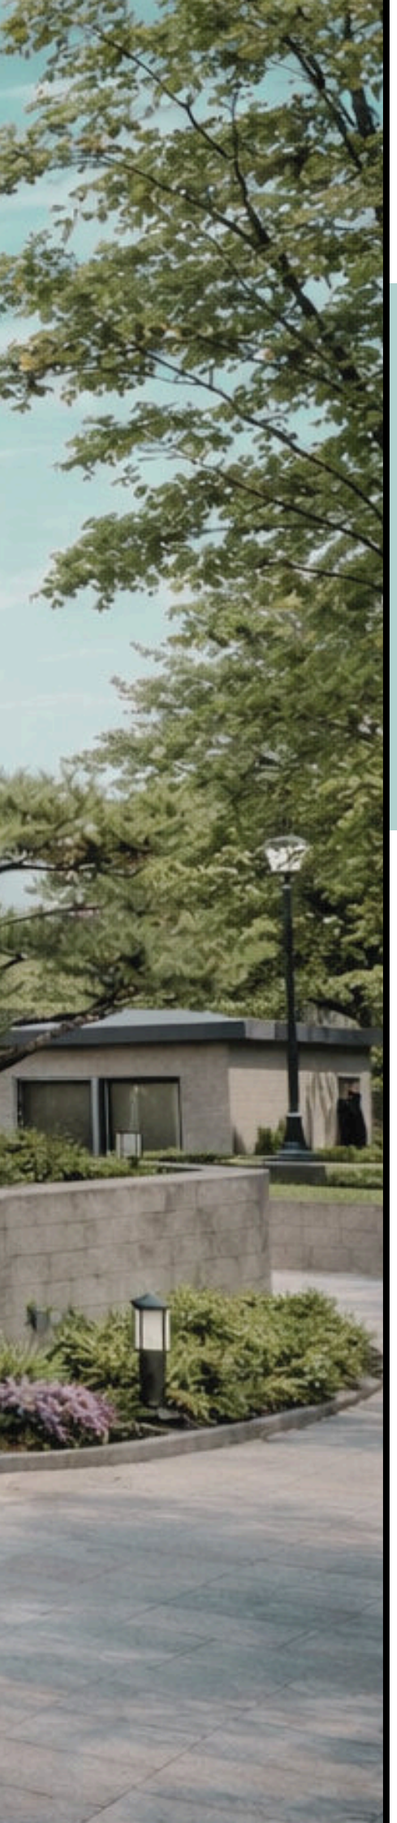


SANSKRITI MILON KENDRA

Kalyani, West Bengal

In a city that gathers to perform, to celebrate, to mourn, and simply to be together, the question this building asked was not how large a stage should be, but how generously a building can give itself to the people around it. The Sanskriti Milon Kendra begins as a single solid volume heavy, grounded, and certain and is then opened up strategically, carved away at its edges to create thresholds, courtyards, and passages that draw the public in before they have even bought a ticket.

The auditorium at its core is precise and acoustically resolved, designed for performance at the highest level. But wrapped around it is a porous public realm community gathering spaces, multipurpose halls, open display areas that ensures the building is alive even on the days when the stage is dark. Architecture here is not a backdrop for civic life. It is civic life, given form and permanence.

EXPLODED AXONOMETRIC VIEW

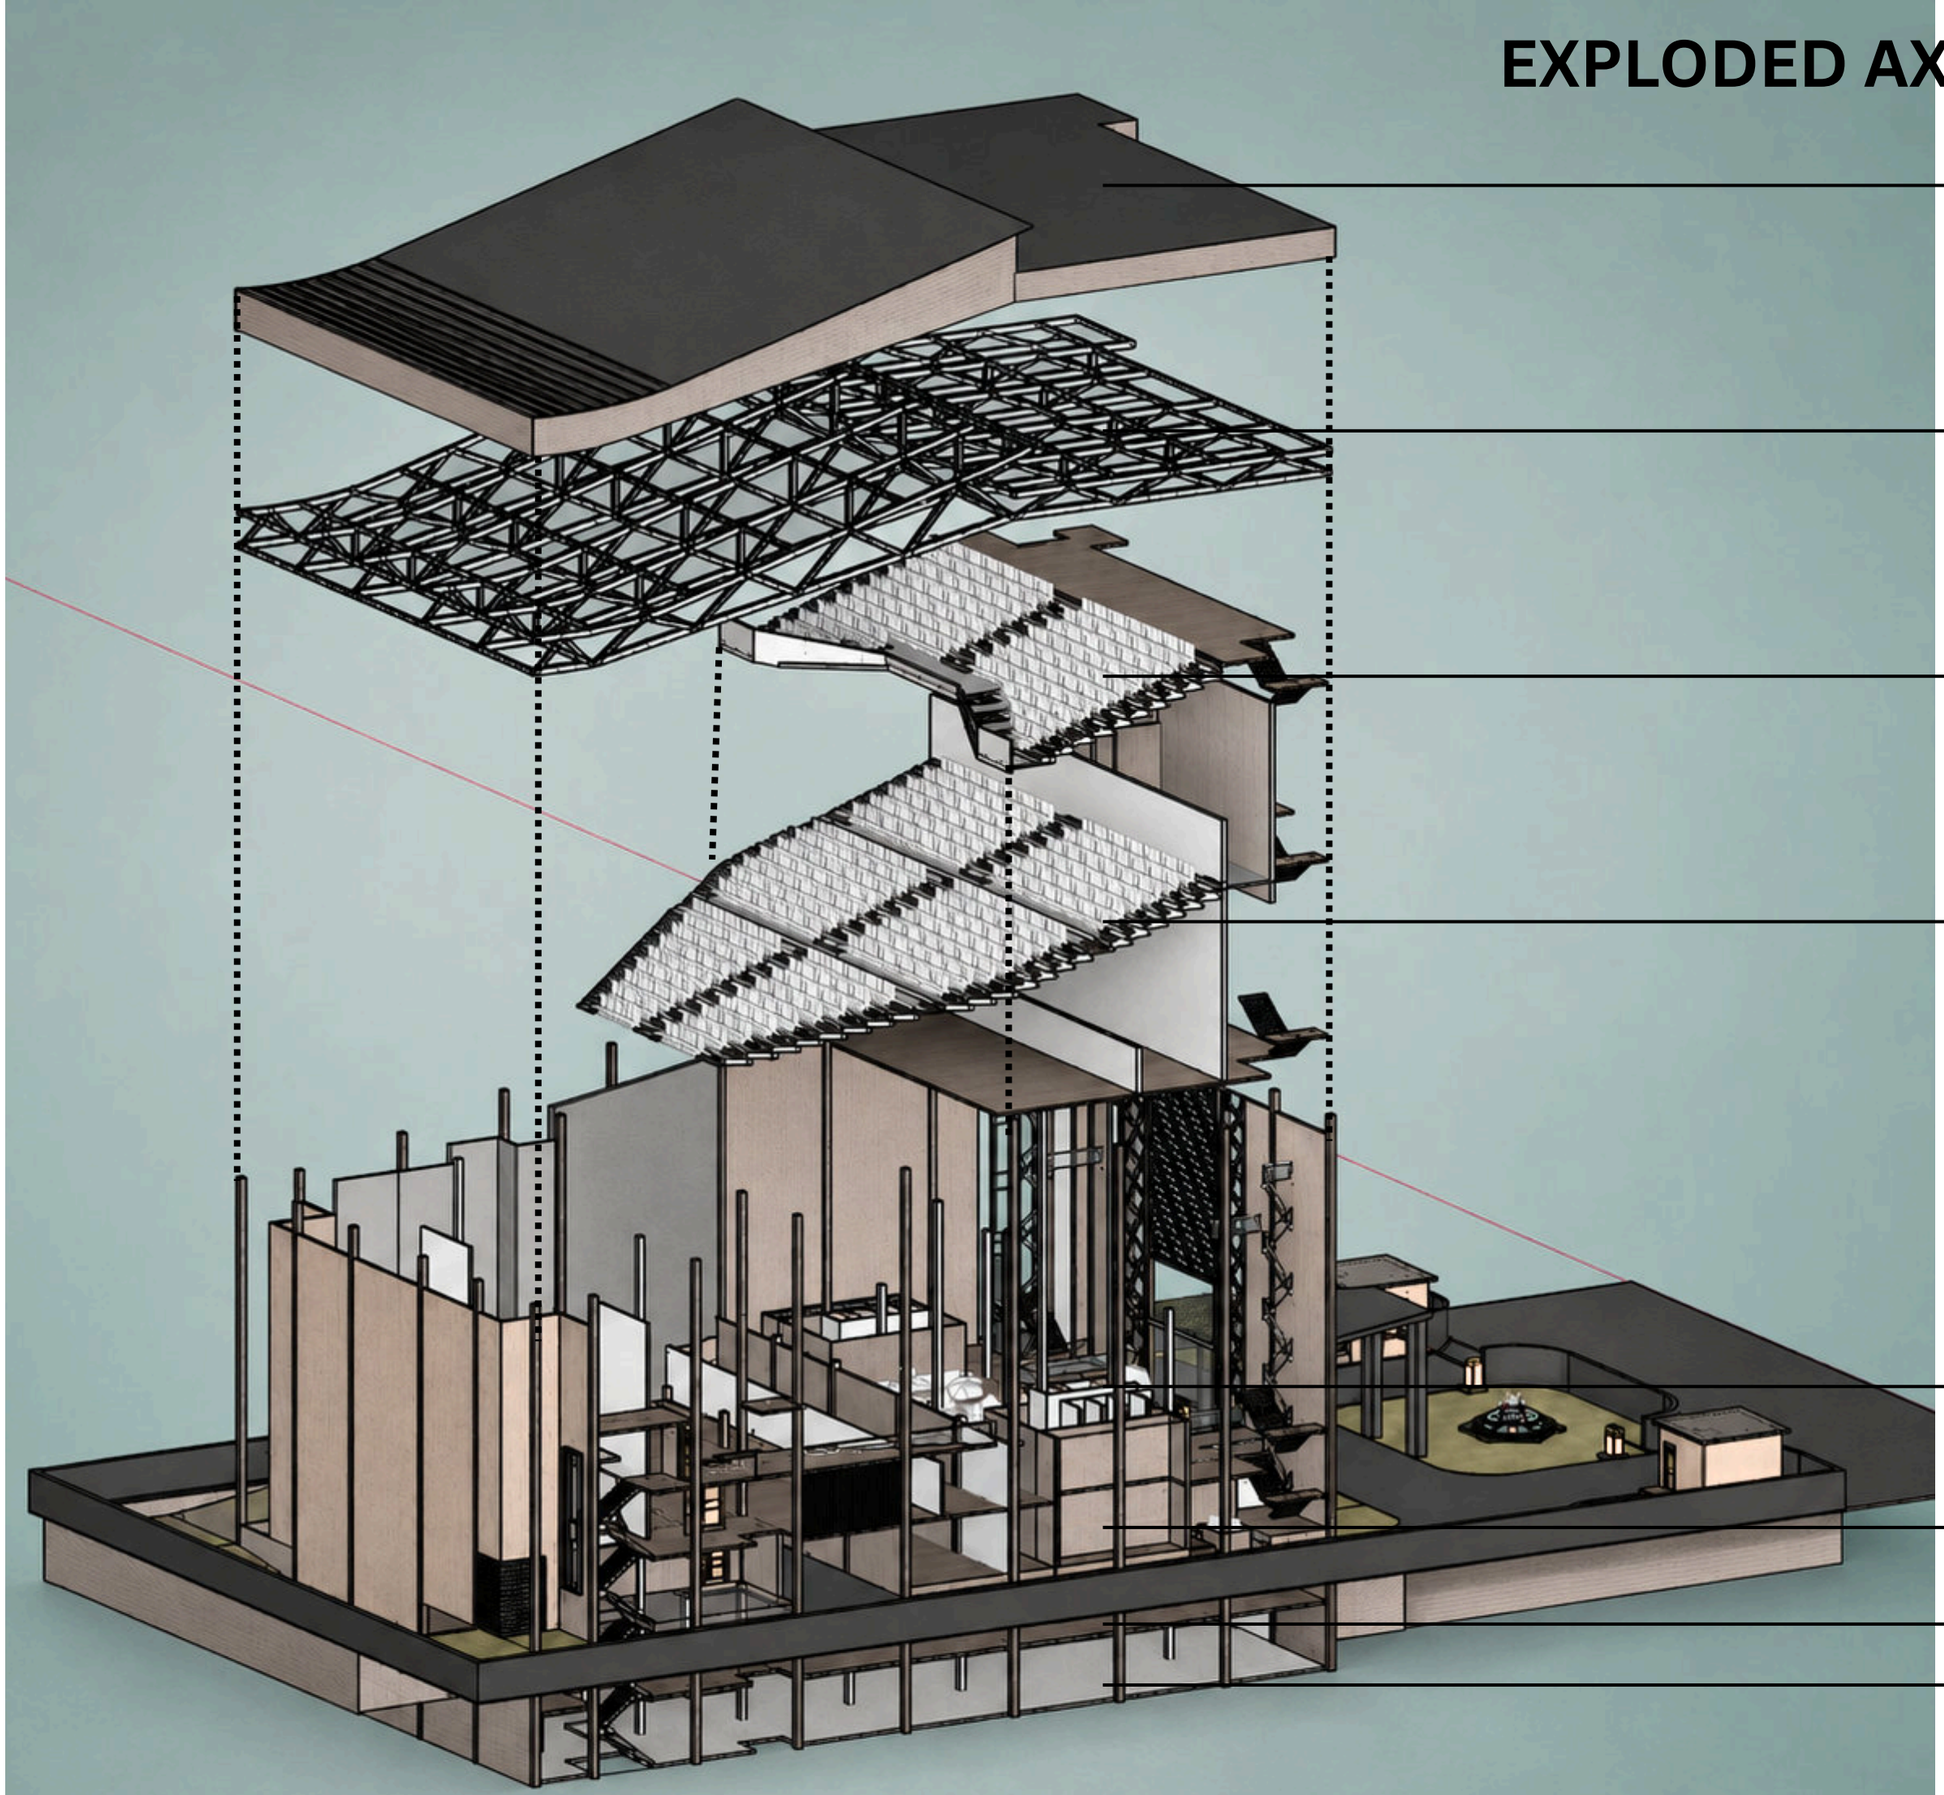

CONCEPT

CARVED MONOLITH

Architecture as Social Landscape

The auditorium-cum-community centre is conceived as a solid monolithic volume emerging from the ground, carved strategically to create spaces for light, movement, and social interaction. The design balances a protected performance core with an open, porous public realm.

SOLID VS VOID



LIGHT STRATEGY




MOVEMENT FLOW




PUBLIC INTERFERANCE




BASIC MASSING

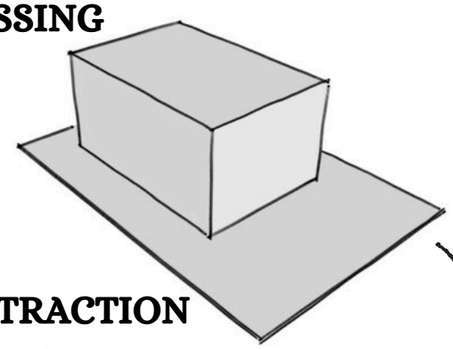


SUBTRACTION FOR PASSAGE

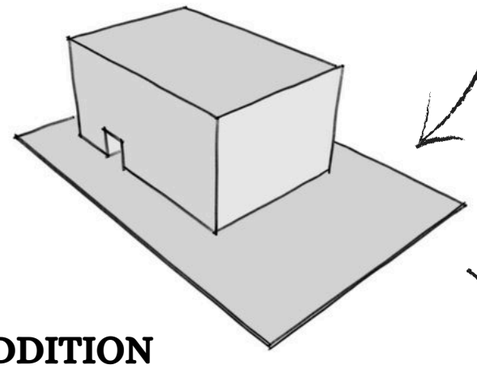

ADDITION OF MASS

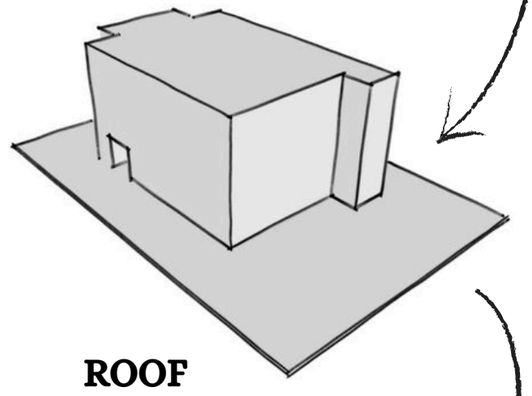


ROOF TRANSFORMATION

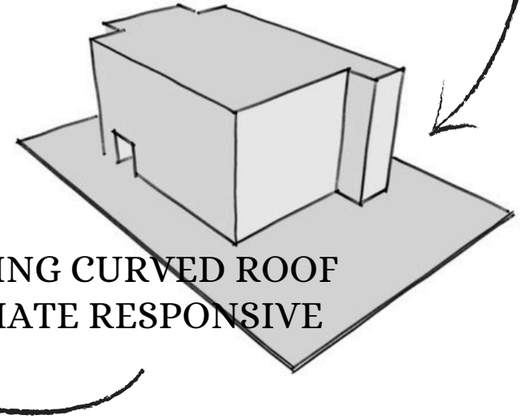


SLOPING CURVED ROOF
CLIMATE RESPONSIVE

HORIZONTAL ARTICULATION

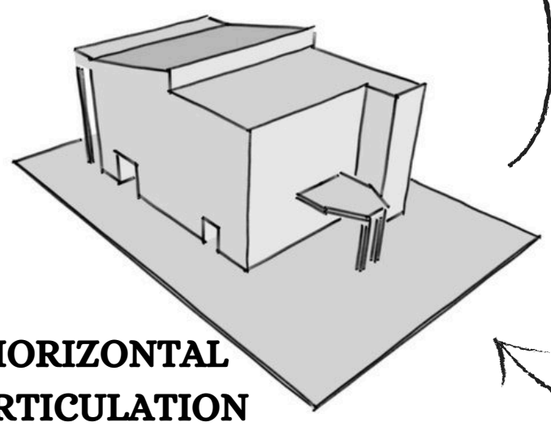


FACADE DEVELOPMENT

LOUVERS, SCREENS AND PATTERNED PANELS

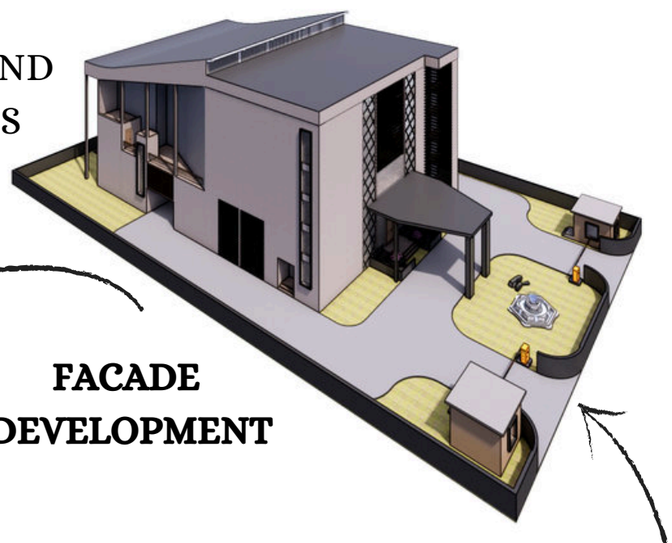


LANDSCAPE INTEGRATION

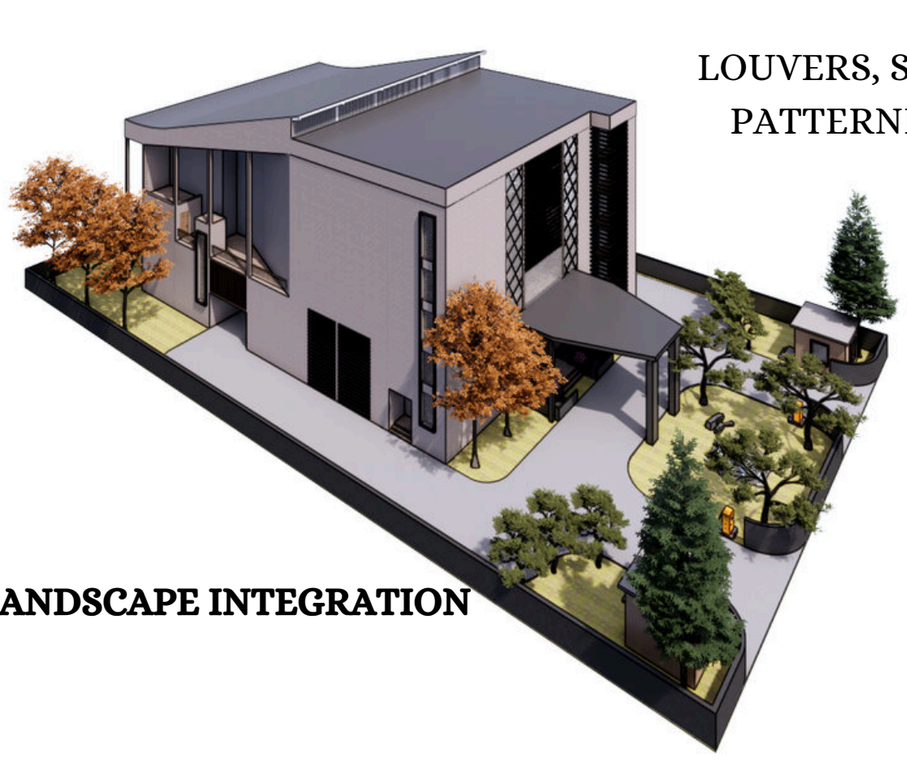


FORM DEVELOPMENT


FLOOR PLANS

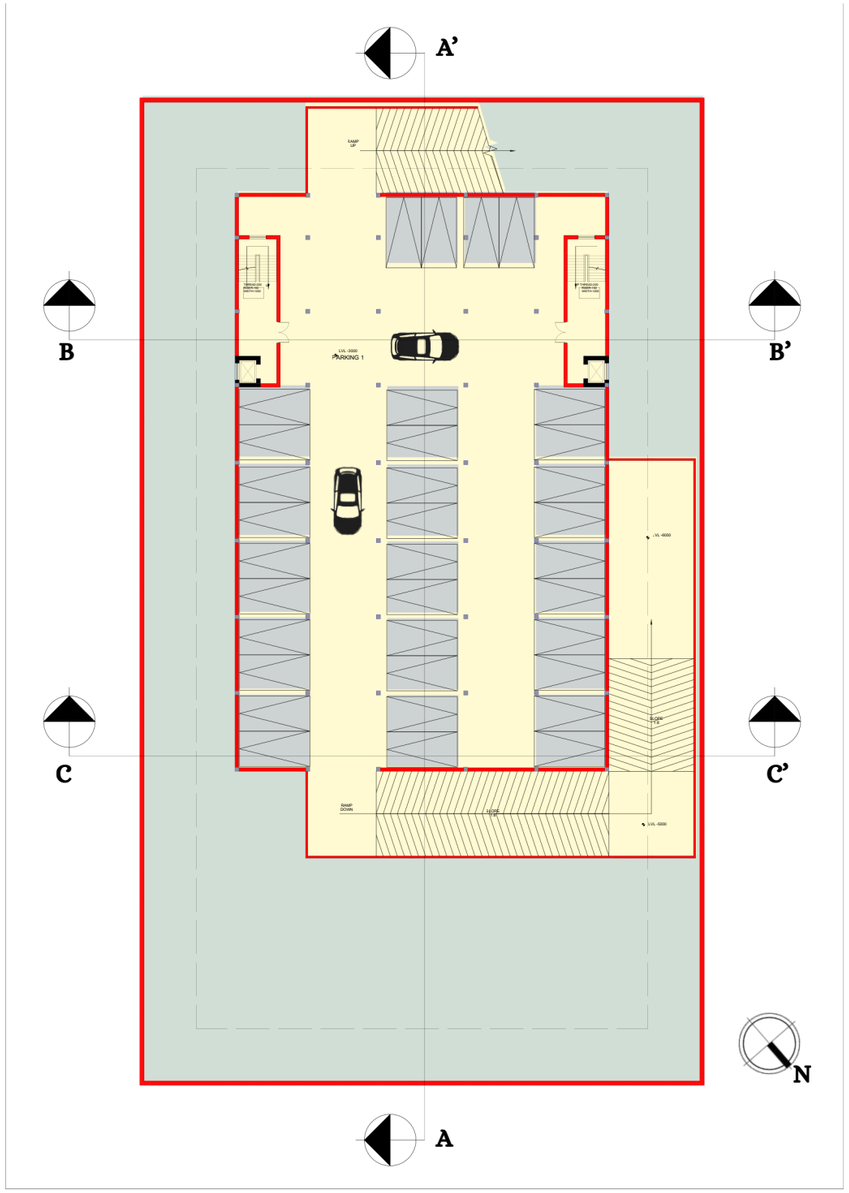


BASEMENT - 1 PLAN
PLAN FROM LVL -2100

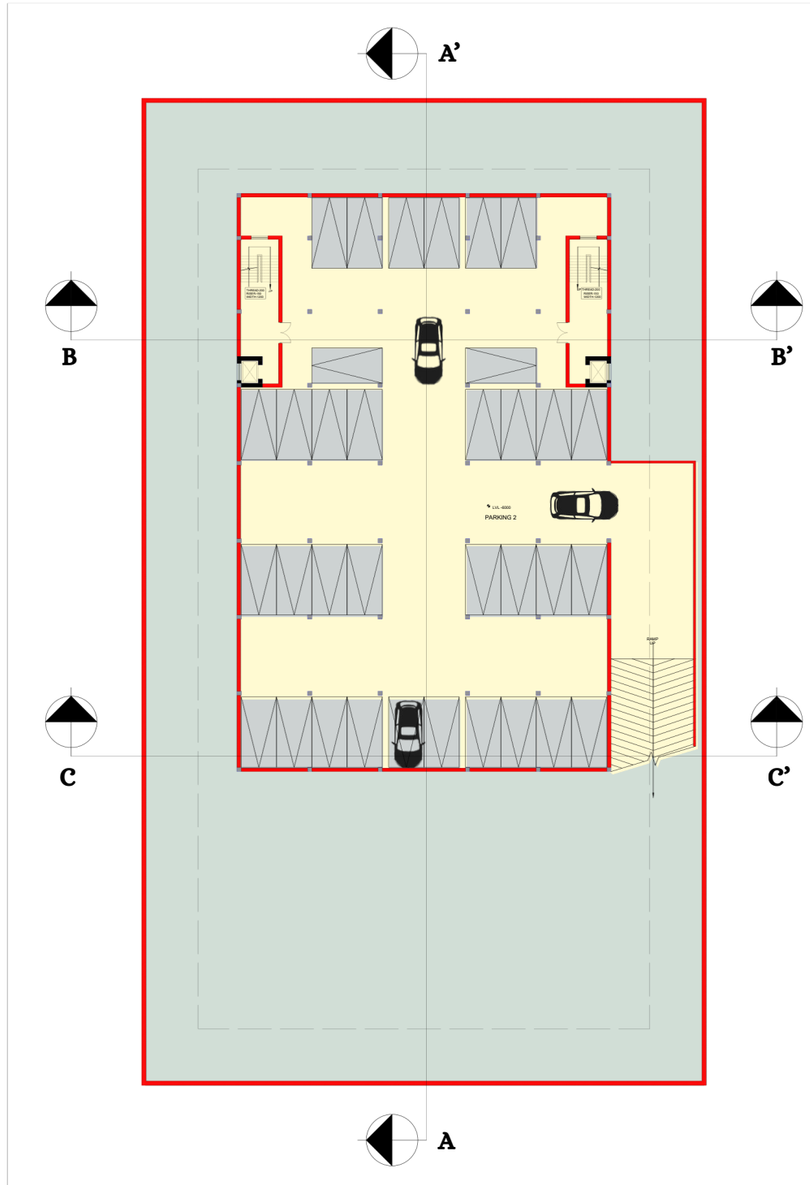


BASEMENT - 2 PLAN
PLAN FROM LVL -5100

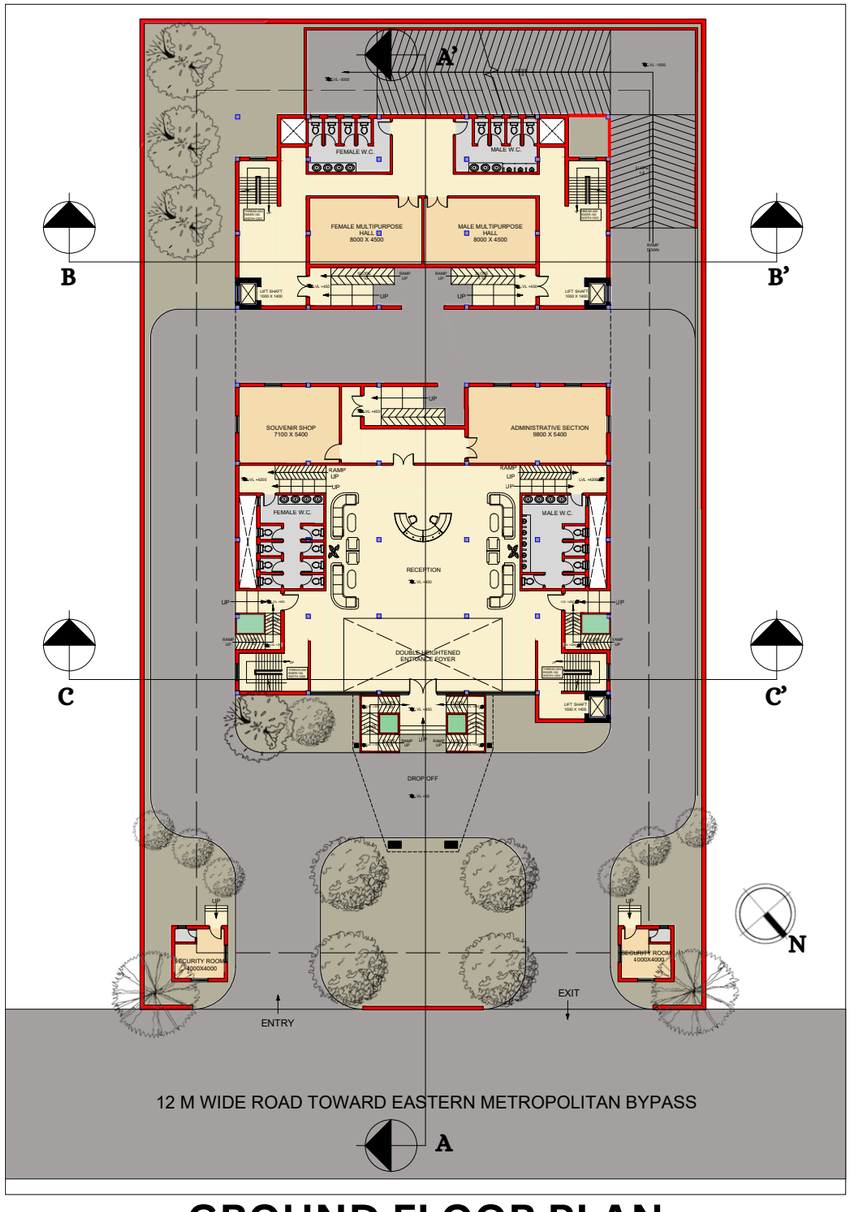


GROUND FLOOR PLAN
PLAN FROM LVL +1350

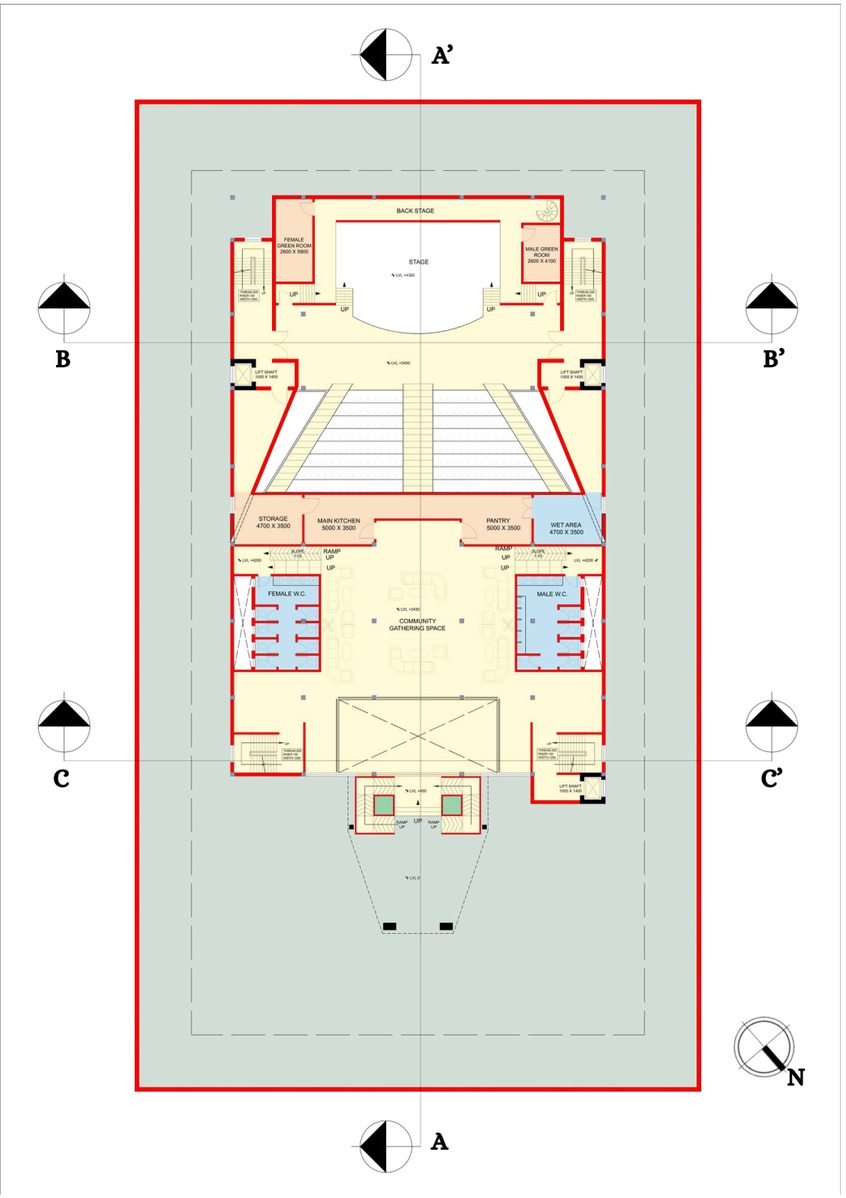

FIRST FLOOR PLAN
PLAN FROM LVL +4350

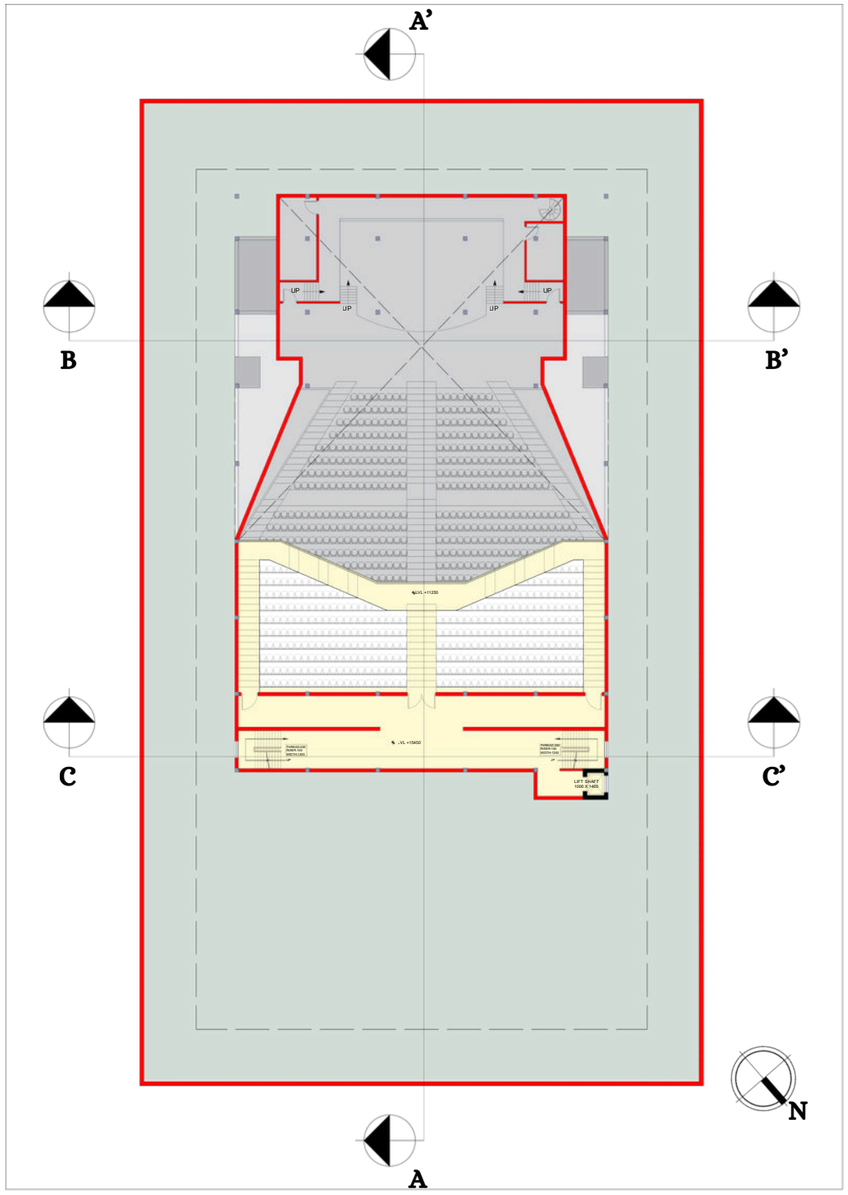


AUDITORIUM PLAN
PLAN FROM LVL +11250

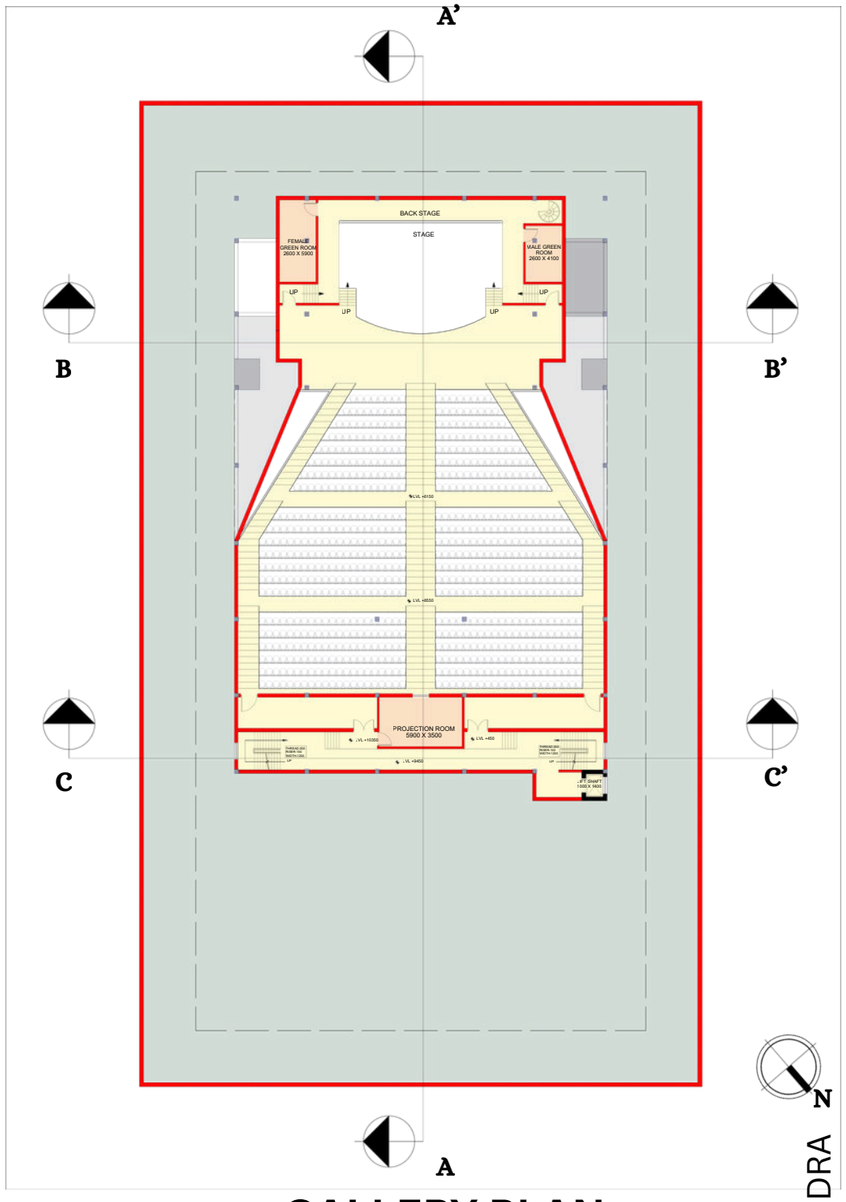


GALLERY PLAN
PLAN FROM LVL +16350


SECTION AA’

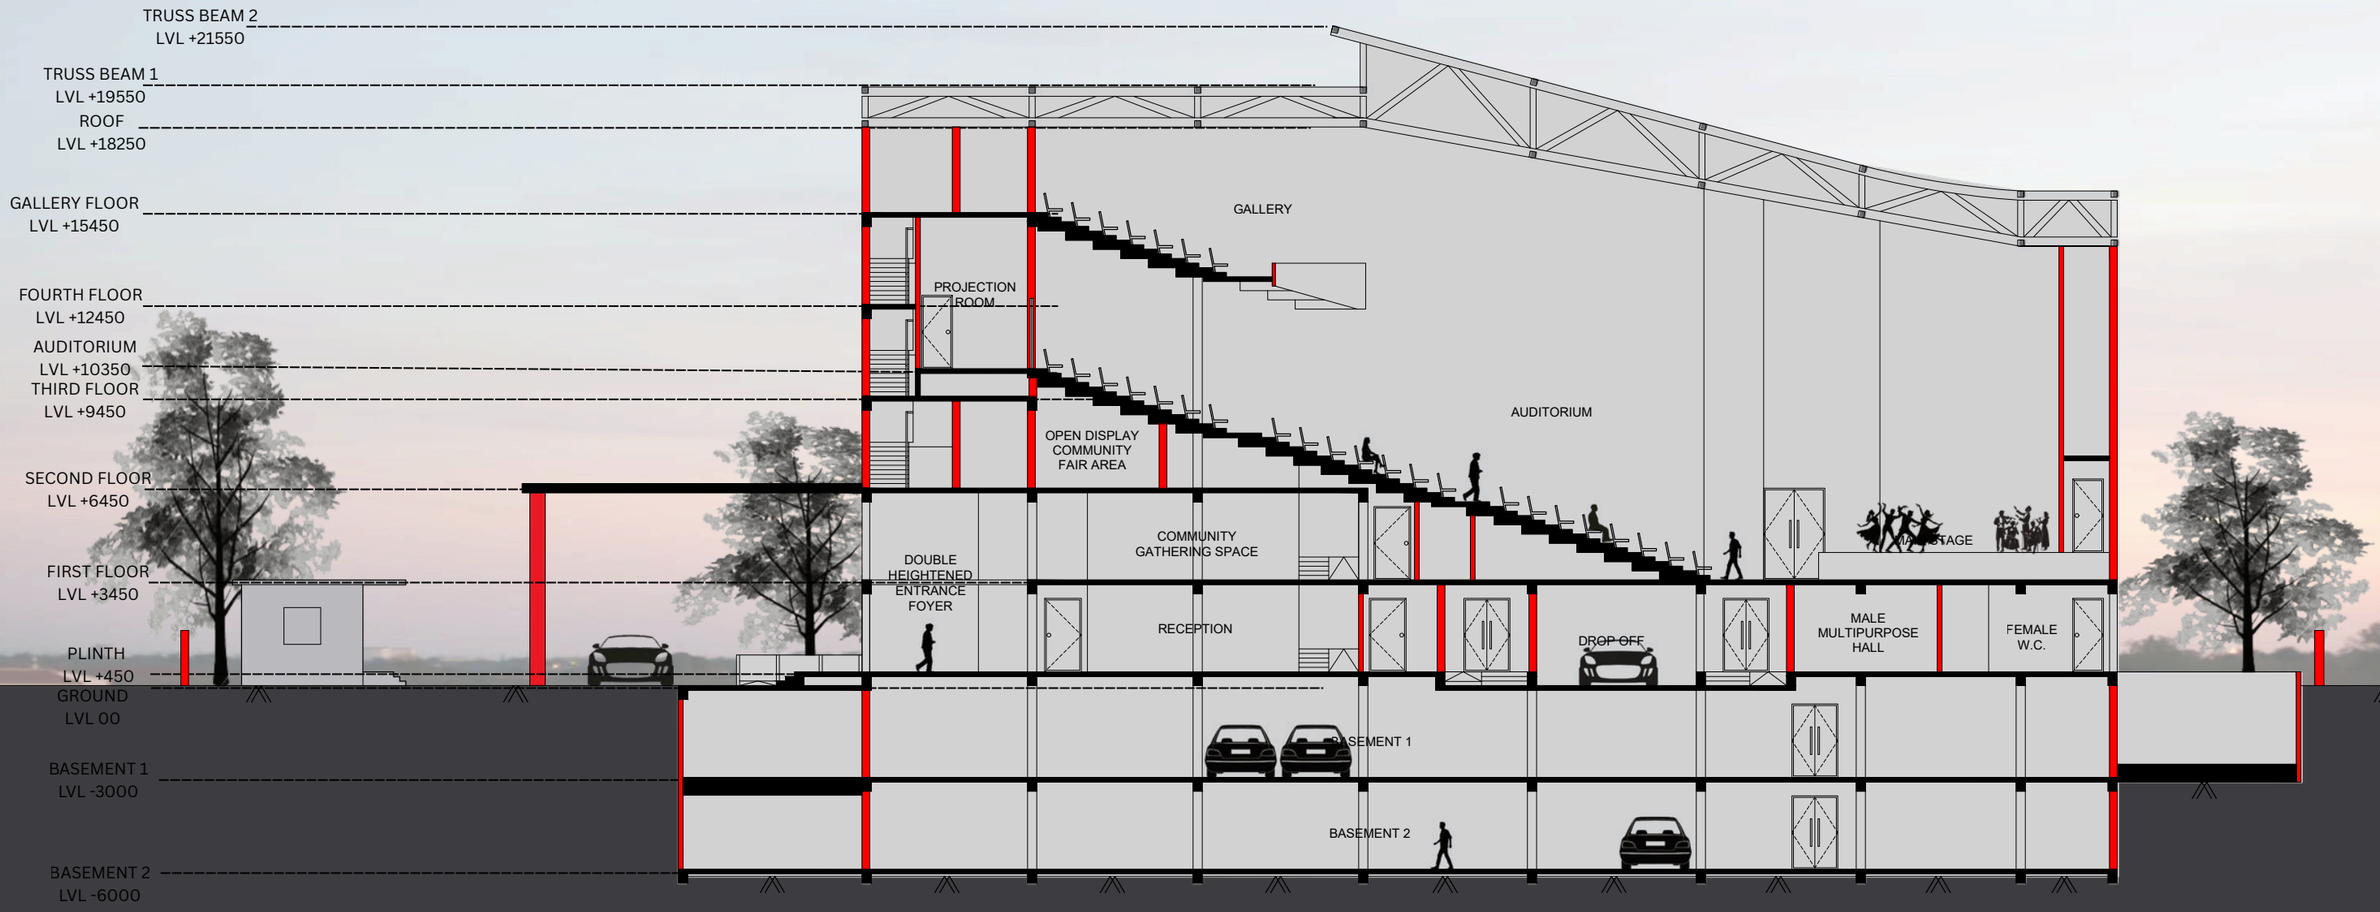
TRUSS BEAM 2
LVL +21550
TRUSS BEAM 1
LVL +19550
ROOF
LVL +18250
GALLERY FLOOR
LVL +15450
FOURTH FLOOR
LVL +12450
AUDITORIUM
LVL +10350
THIRD FLOOR
LVL +9450
SECOND FLOOR
LVL +6450
FIRST FLOOR
LVL +3450
PLINTH
LVL +450
GROUND
LVL 00
BASEMENT 1
LVL -3000
BASEMENT 2
LVL -6000
GALLERY
PROJECTION ROOM
AUDITORIUM
OPEN DISPLAY COMMUNITY FAIR AREA
COMMUNITY GATHERING SPACE
DOUBLE HEIGHTENED ENTRANCE FOYER
RECEPTION
DROP OFF
MALE MULTIPURPOSE HALL
FEMALE W.C.
BASEMENT 1
BASEMENT 2

SECTION BB’

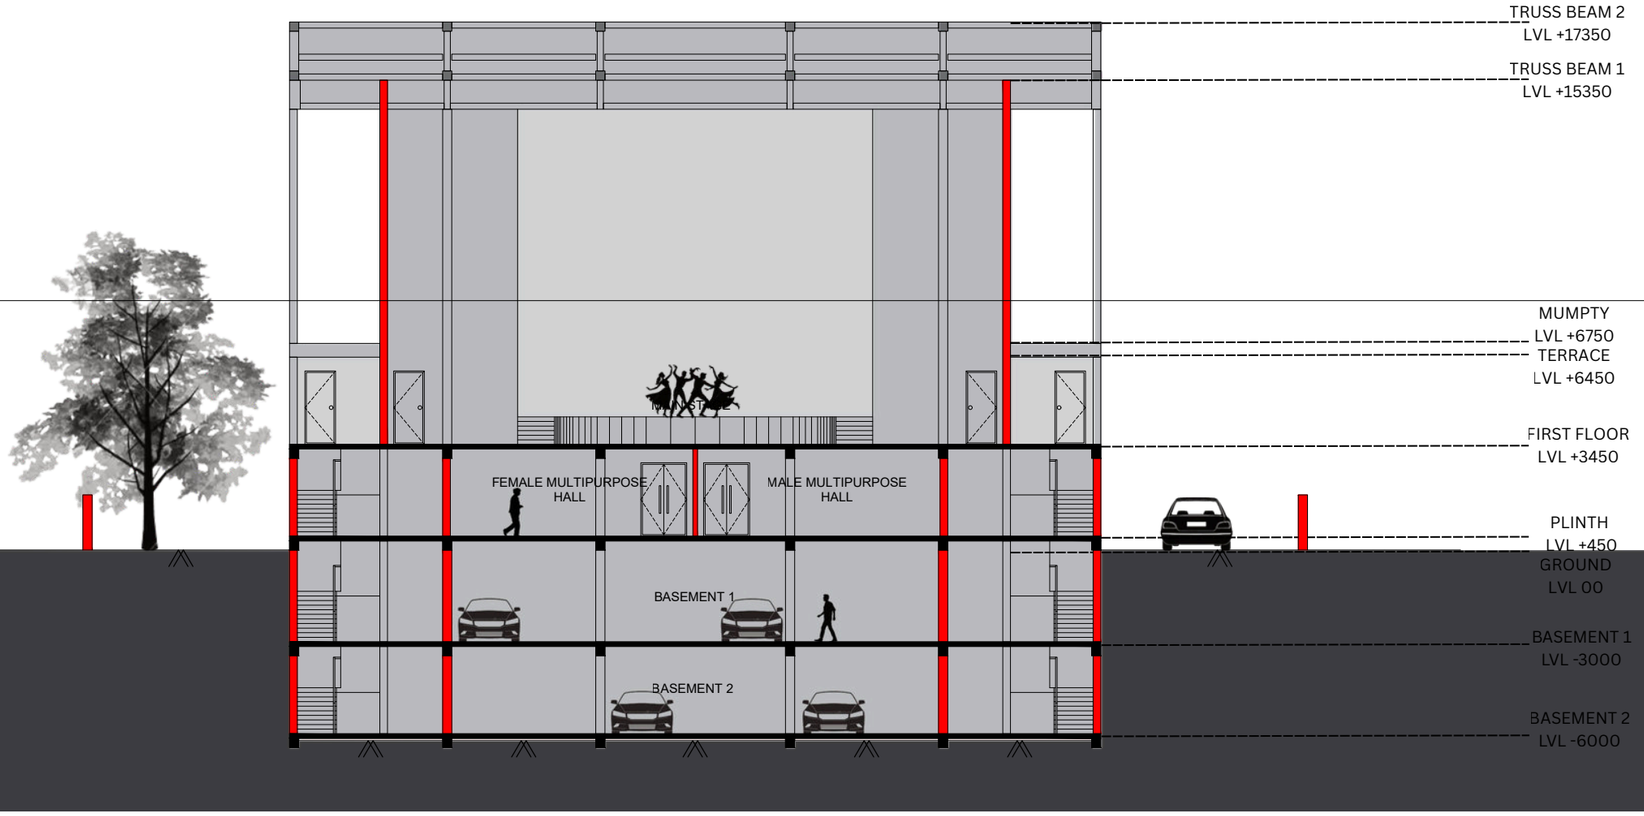

SECTION CC’

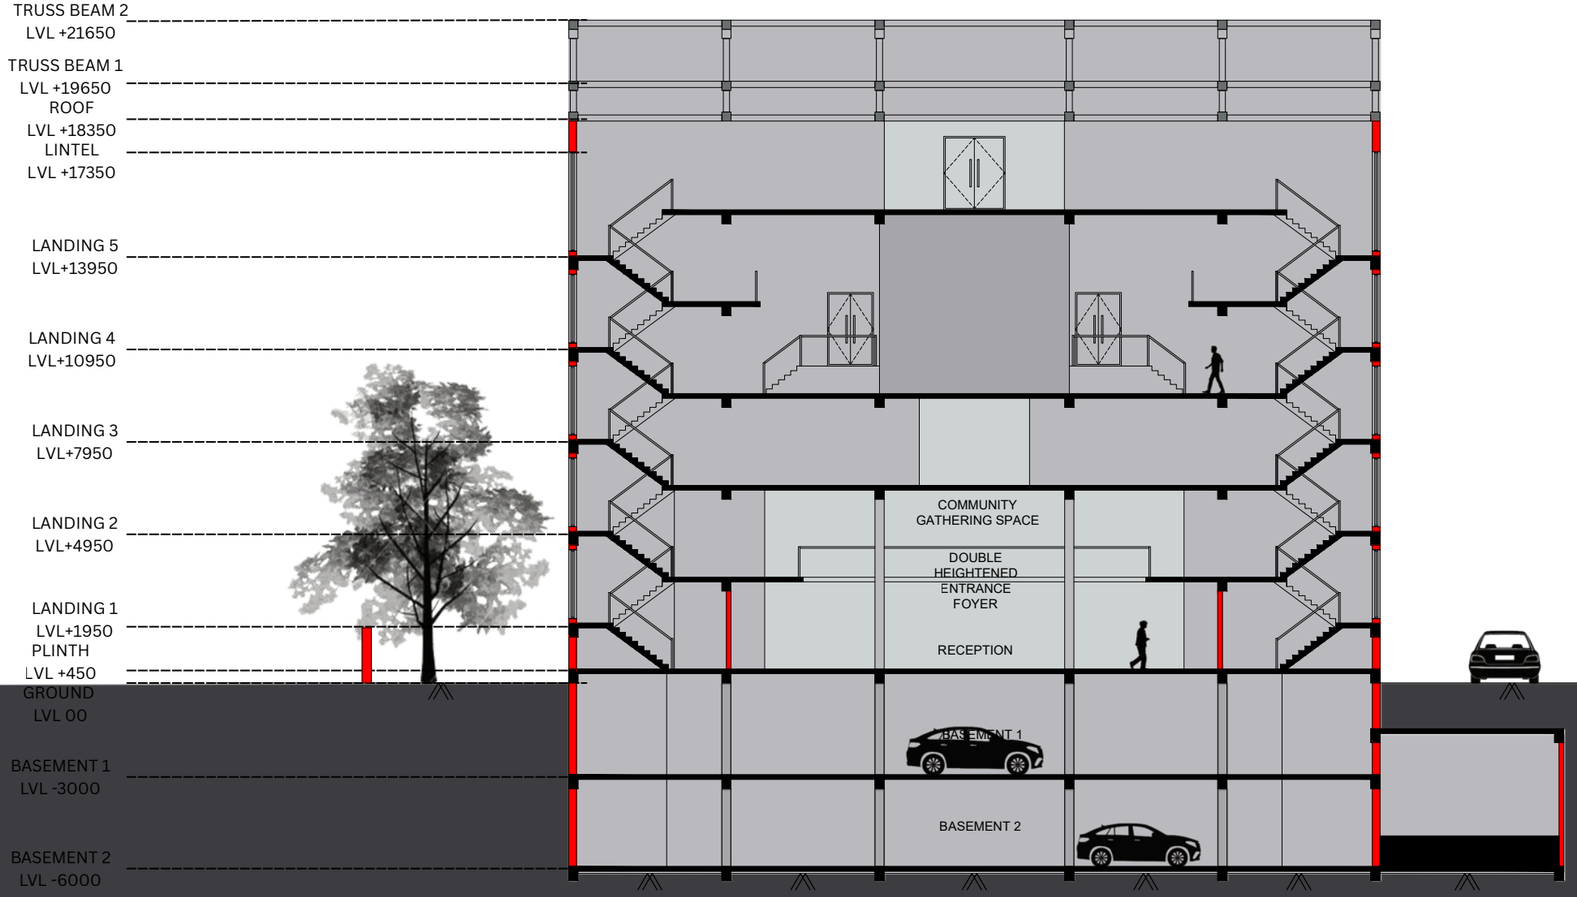











WORKING DRAWING

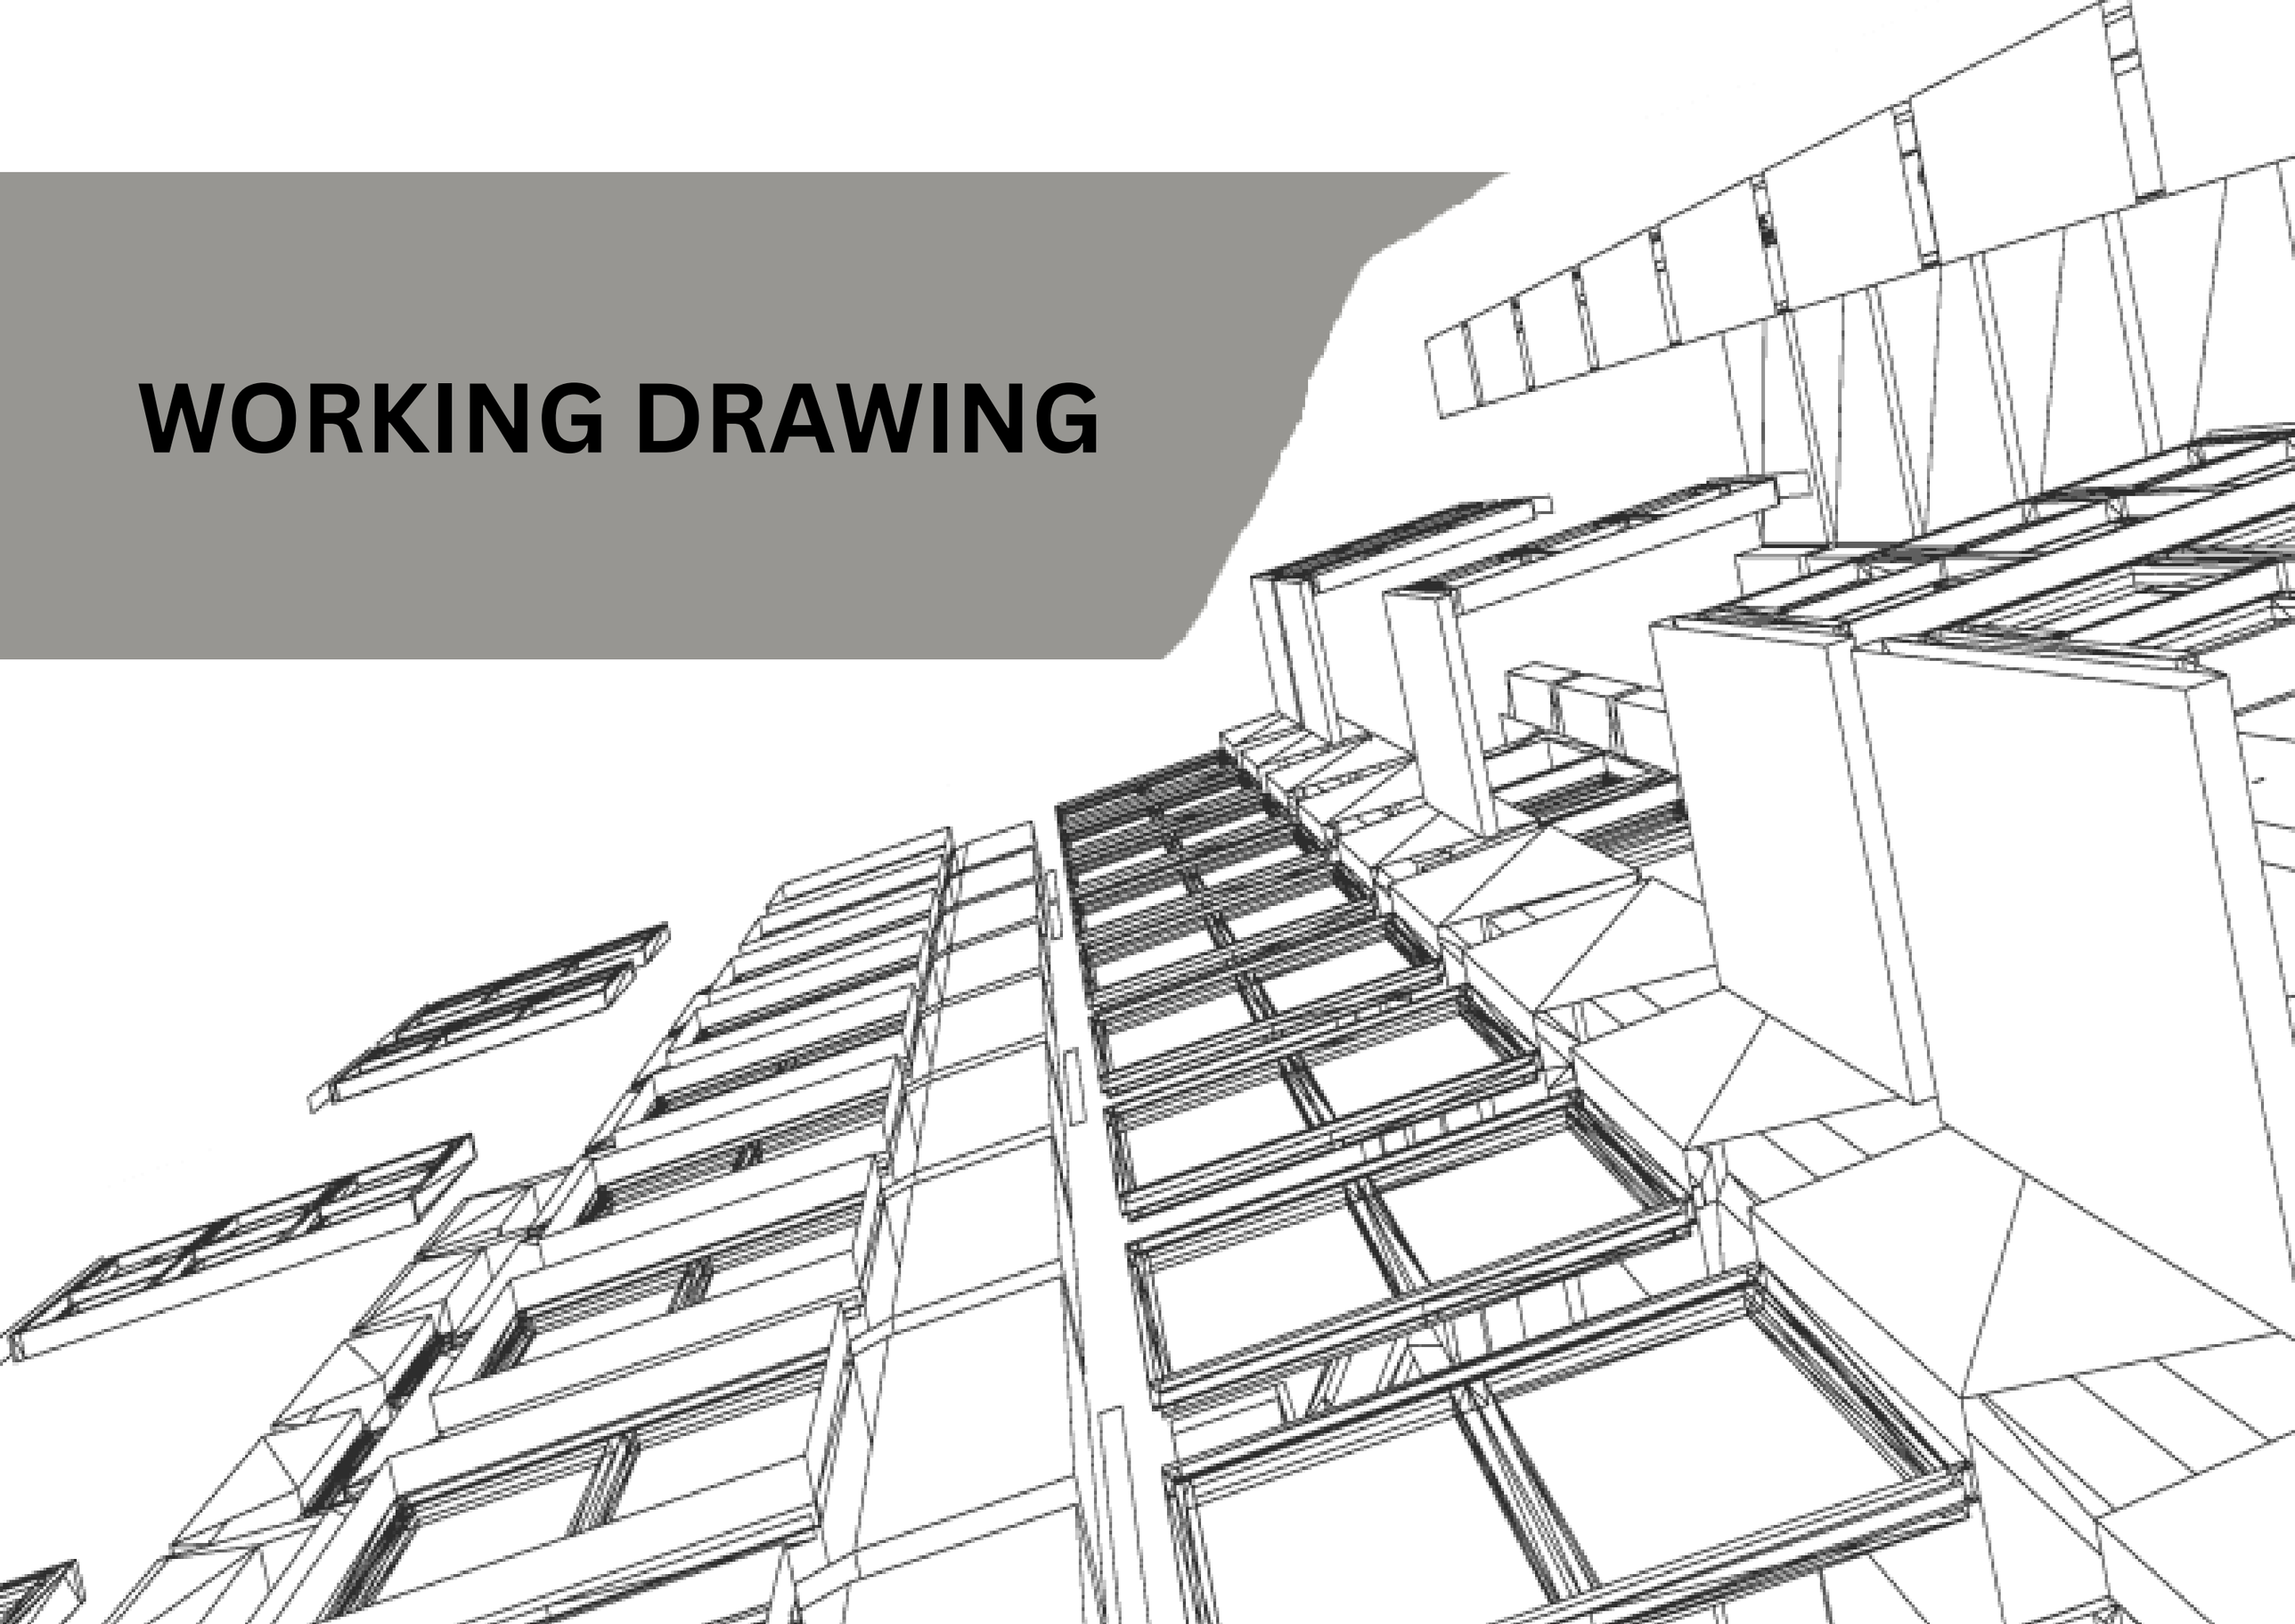

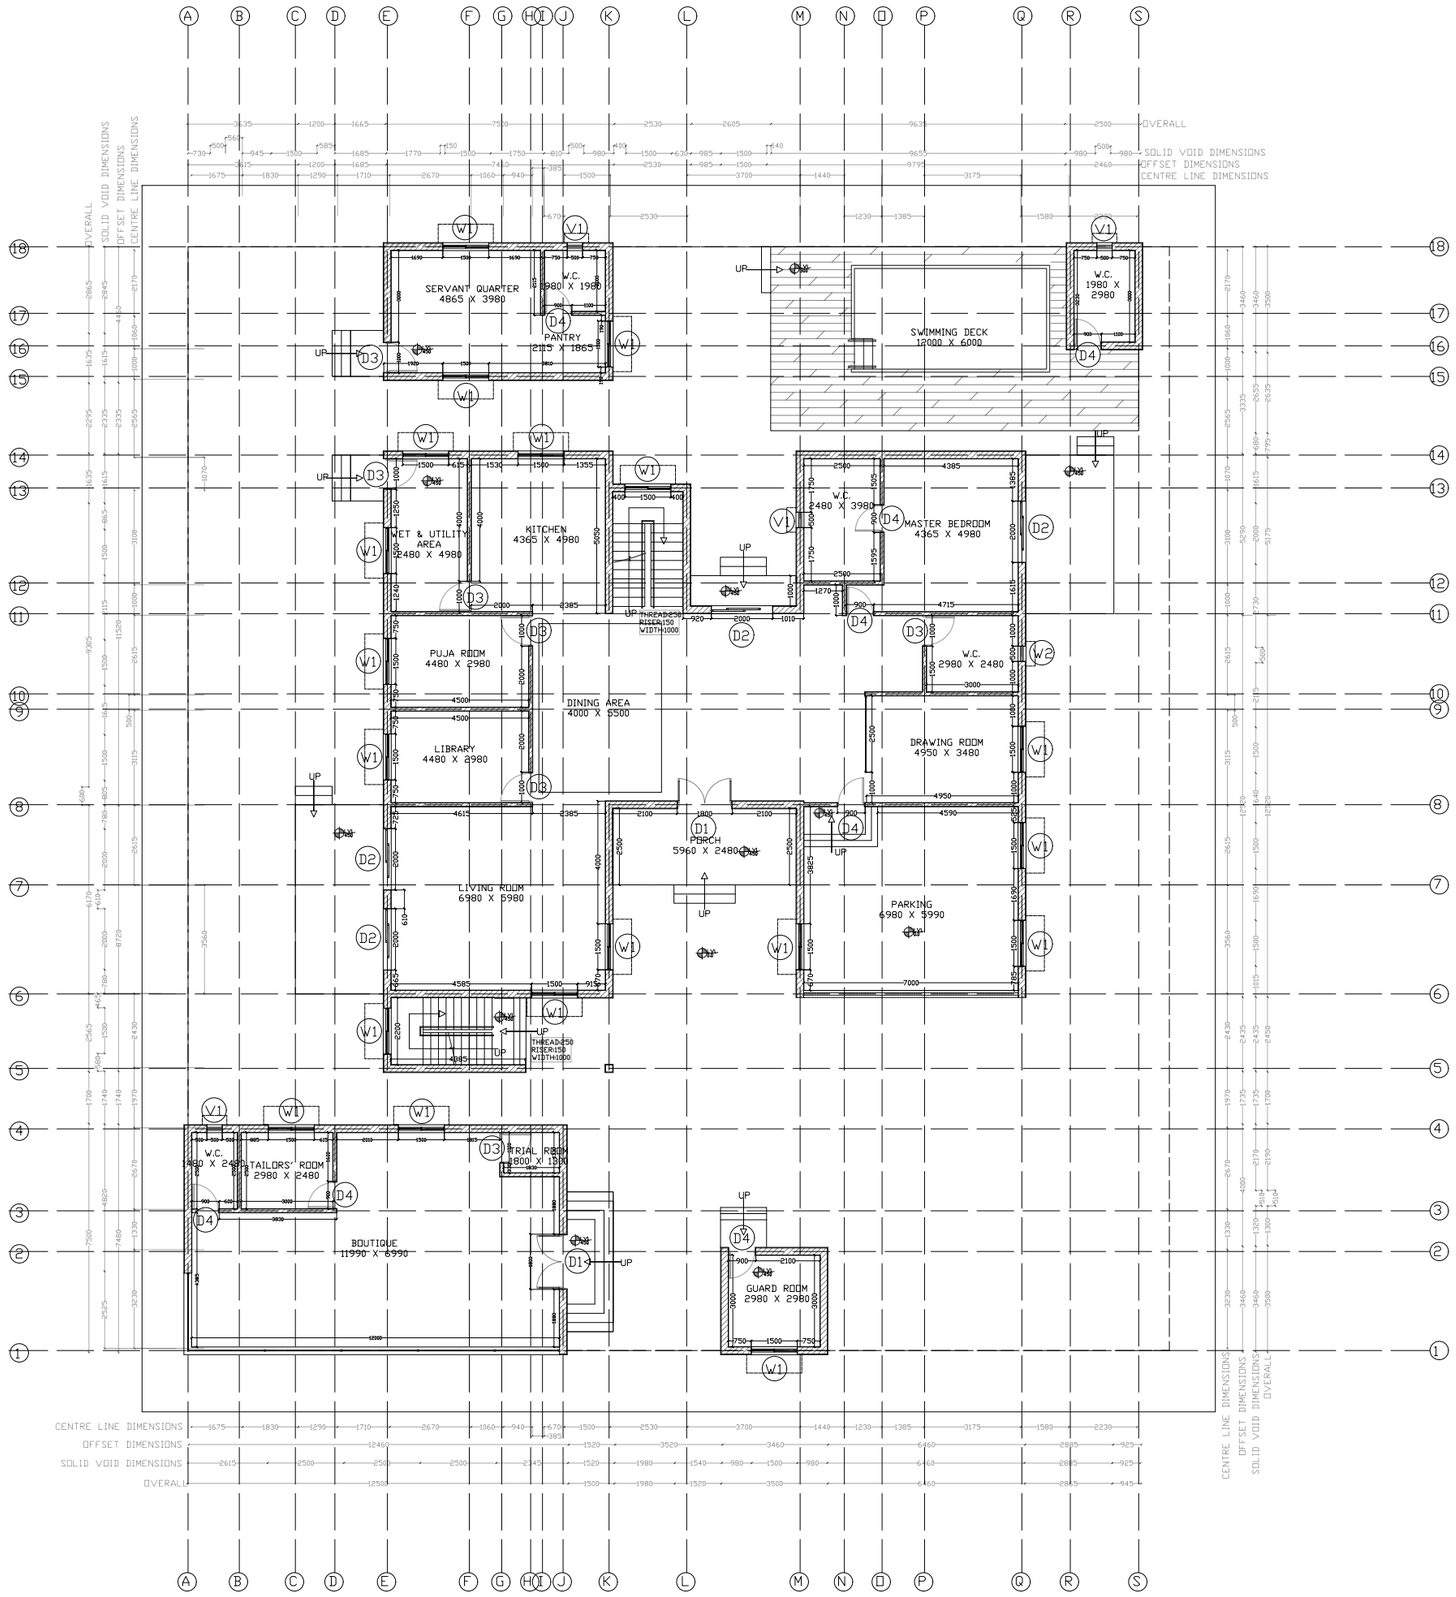

DOOR AND WINDOW SCHEDULE									
SR. NO.	TYPE	OPENING SIZE				FINIISH SIZE				MATERIAL
	DOOR, WINDOW, VENTILATOR	LINTEL	SILL	HEIGHT	WIDTH	LINTEL	SILL	HEIGHT	WIDTH	
1.	D1	2400	0	2400	1800	2400	0	2350	1700	D1
2.	D2	2400	0	2400	2000	2400	0	2350	1900	D2
3.	D3	2400	0	2400	1000	2400	0	2350	900	D3
4.	D4	2400	0	2400	900	2400	0	2350	800	D4
5.	W1	2400	600	1800	1500	2400	600	1700	1400	W1
6.	V1	2400	1800	600	500	2400	1800	500	400	V1

GENERAL NOTES:

1. All dimensions are in mm unless specified otherwise Figured
2. dimensions shall supersede measurement by scale Drawings
3. shall be read in conjunction with contracts, term and condition; Specifications; Schedule of items and other drawings. All openings are masonary openings. All brick work
4. shall be done with 1:6 cement mortar. All half brick shall be done
5. with 1:4 cement mortar. PCC used shall be 1:2:4**.** Drawings are not to
6. be scaled. All 75th brick shall be done with 1:3 cement mortar.
7. Chicken wire mesh shall be provided at the junction of different
8. components of building of different
9. materials prior to plastering.
10.

PROJECT:
RESIDENCE

WORKING DRAWING

GROUND FLOOR PLAN

DESIGNED & DRAWN BY:
VISHAKHA BHARTI
(23AR10029)

CHECKED BY:
PROF. SHREYAS BHARULE

DATE: 26/08/2025

SCALE- 1:100

N


DRAWING NO.
AR 02

REVISION NO.
00


SECTION AA'




SECTION BB'

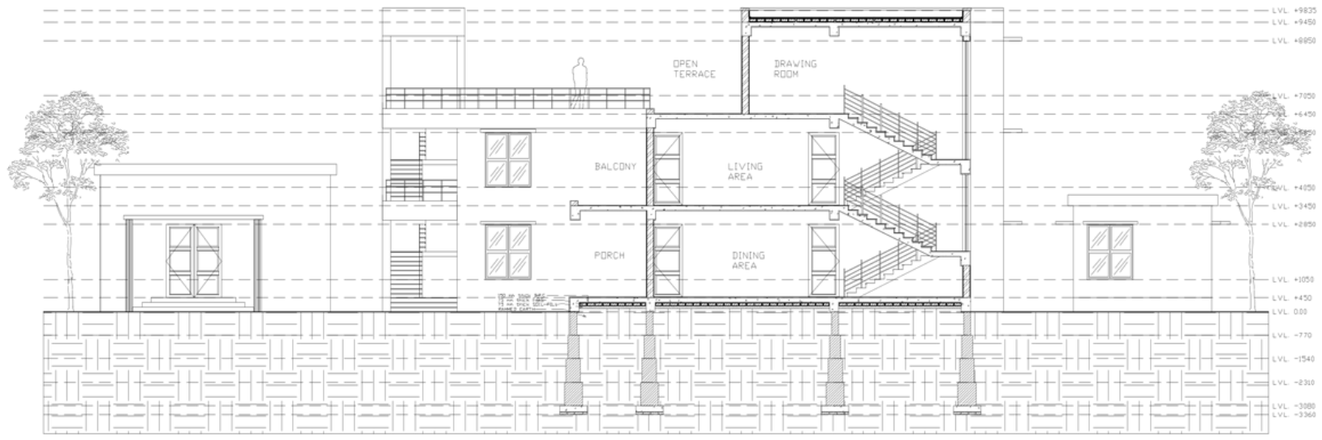

SECTION CC'

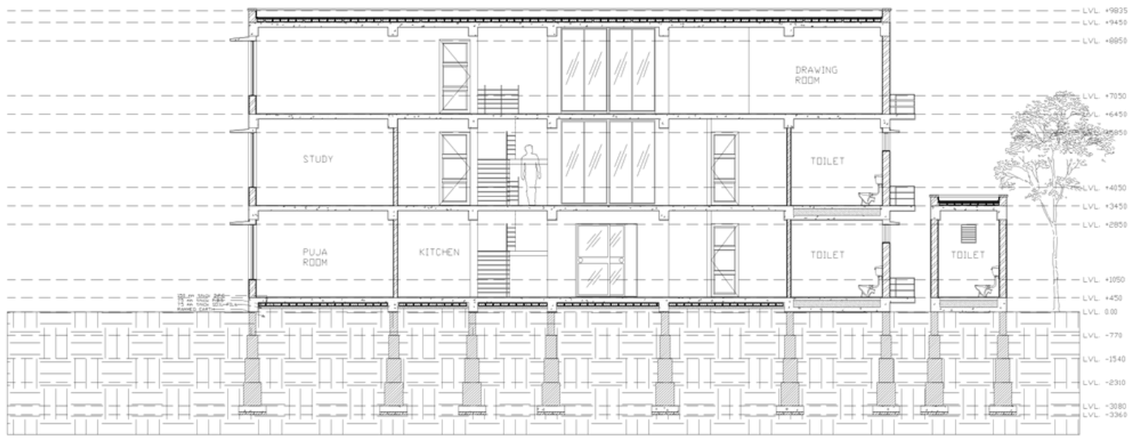

KEY PLAN

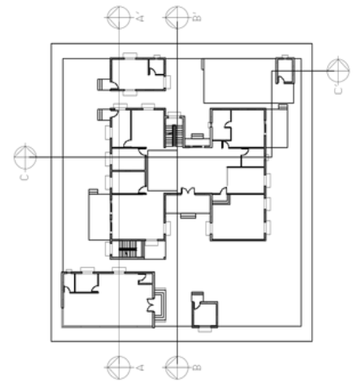

GENERAL NOTES:

1. Alldimensionsare in mm unless specified otherwise
2. Figured dimensions shall supersede measurement by scale
3. Drawings shall be read in conjunction with contracts, term and condition; Specifications; Schedule of items and other drawings.
4. All openings are masonary openings.
5. All brick work shall be done with 1:6 cement mortar.
6. All half brick shall be done with 1:4 cement mortar.
7. PCC used shall be 1:2:4**.**
8. Drawingsarenottobescaled.

PROJECT:
RESIDENCE

WORKING DRAWING

BUILDING SECTION

DESIGNED & DRAWN BY:
VISHAKHA BHARTI
(23AR10029)

CHECKED BY:
PROF. SHREYAS BHARULE


DATE: 13/10/2025

SCALE- 1:100


N

DRAWING NO.
AR 06


REVISION NO.
00

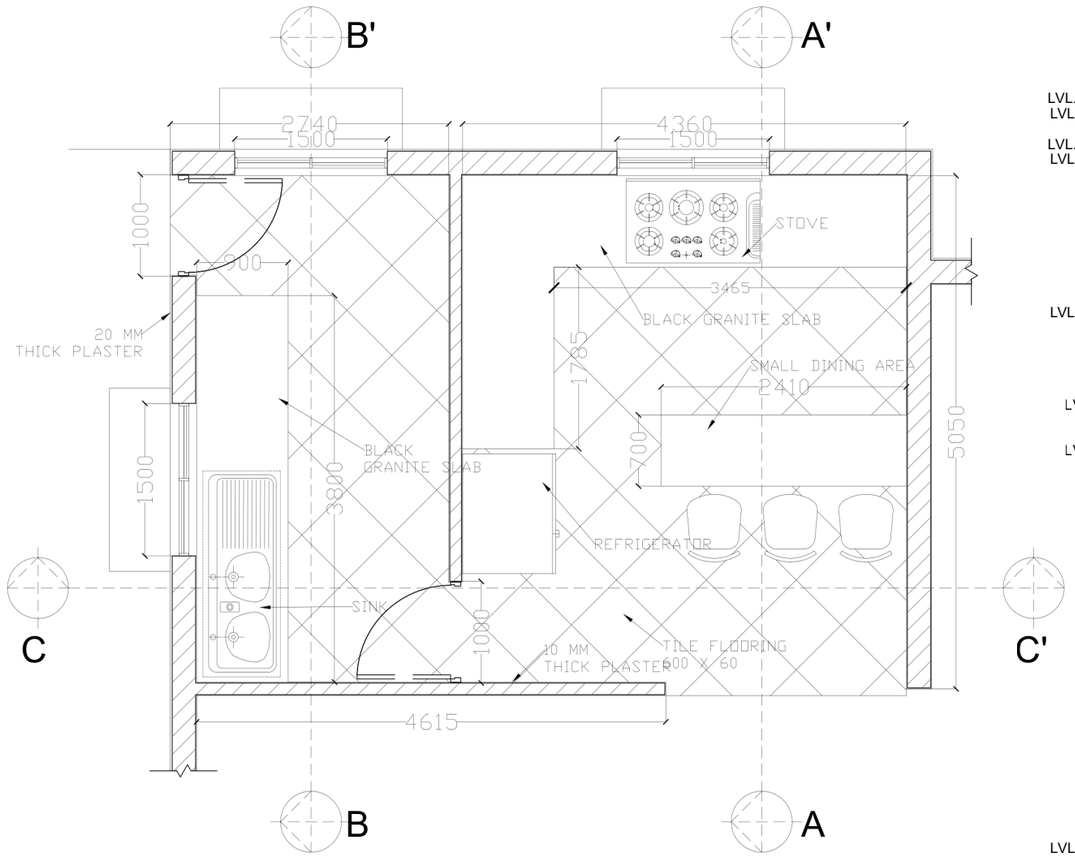


FLOOR PLAN

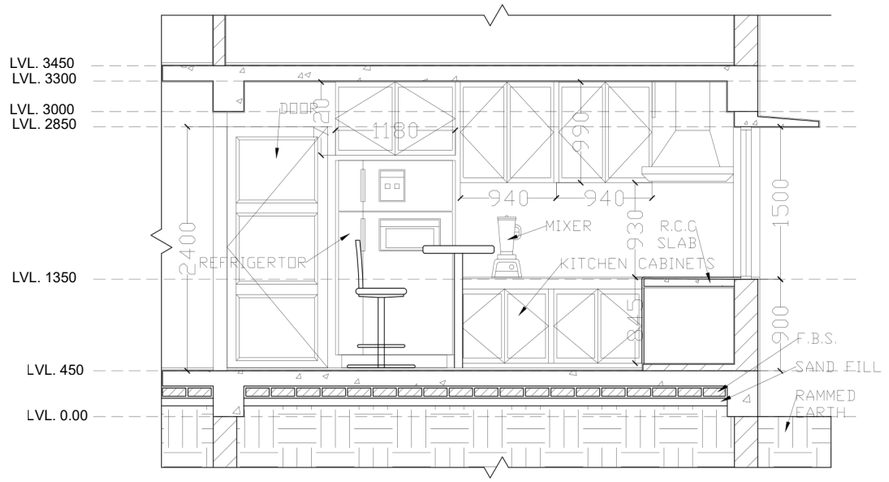

SECTION AA'

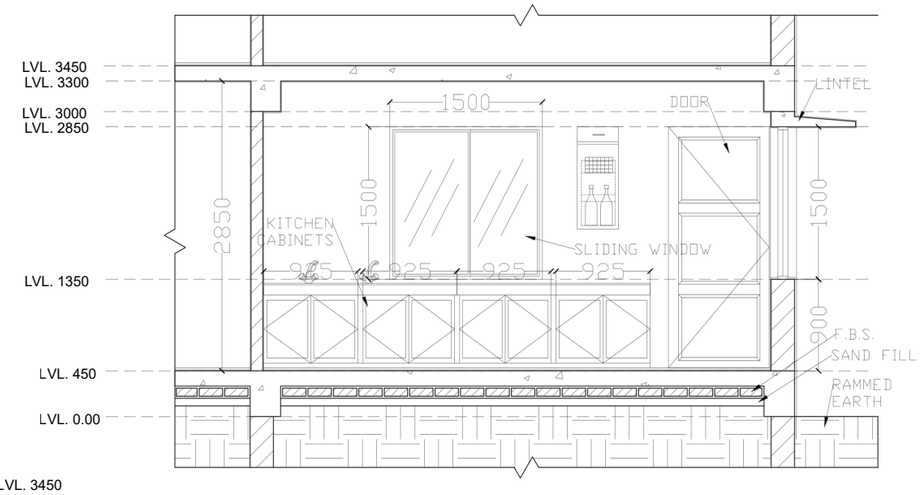


SECTION BB'

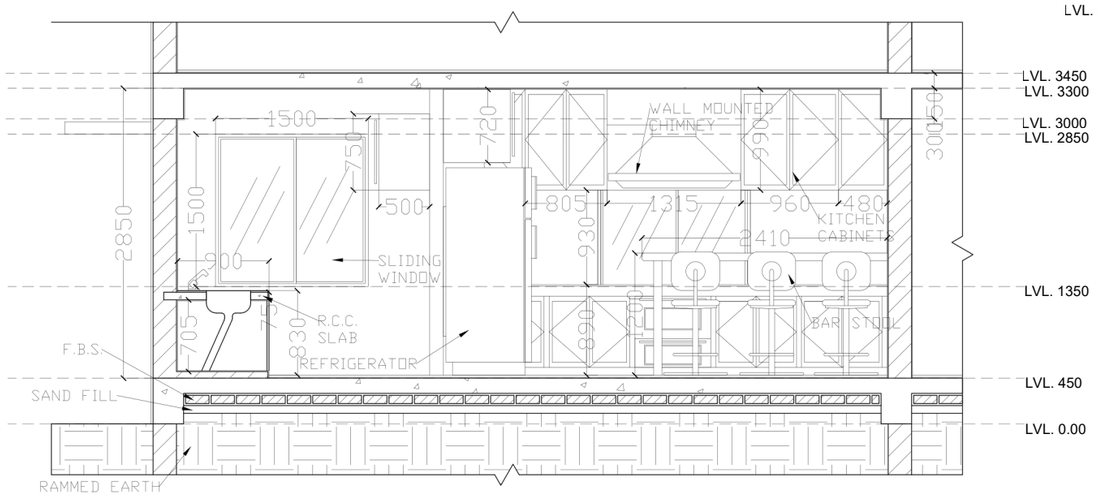

SECTION CC'

KEY PLAN

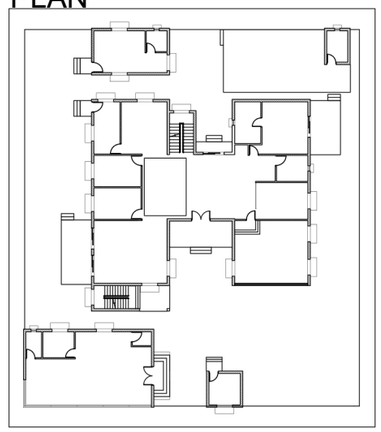

GENERAL NOTES:

1. Alldimensionsare in mm unless specified otherwise
2. Figured dimensions shall supersede measurement by scale
3. Drawings shall be read in conjunction with contracts, term and condition; Specifications; Schedule of items and other drawings.
4. All openings are masonary openings.
5. All brick work shall be done with 1:6 cement mortar.
6. All half brick shall be done with 1:4 cement mortar.
7. PCC used shall be 1:2:4.

Drawingsarenottobescaled.

PROJECT:
RESIDENCE

WORKING DRAWING

KITCHEN DETAILS

DESIGNED & DRAWN BY:
VISHAKHA BHARTI
(23AR10029)

CHECKED BY:
PROF. SHREYAS BHARULE

DATE: 29/10/2025

SCALE- 1:30

N

DRAWING NO.
AR 08

REVISION NO.
00

MISCELLANEOUS

LIVING AREA

WELCOME WALL

COMMISIONED ARTWORK



KALAMKARI TREE OF LIFE

L- CORNER PANEL

DISTRESSED FINISH LAMP

WALL BEADING AND CORNICE DESTAIL







NESTED TABLE



ACCENT CHAIR

STUCCO FINISH FLOOR TILES



WESTERN COLOUR SCHEME



LIME FINISH

LIVING AREA



Until the next idea !

vishakha8642@kgpian.iitkgp.ac.in